


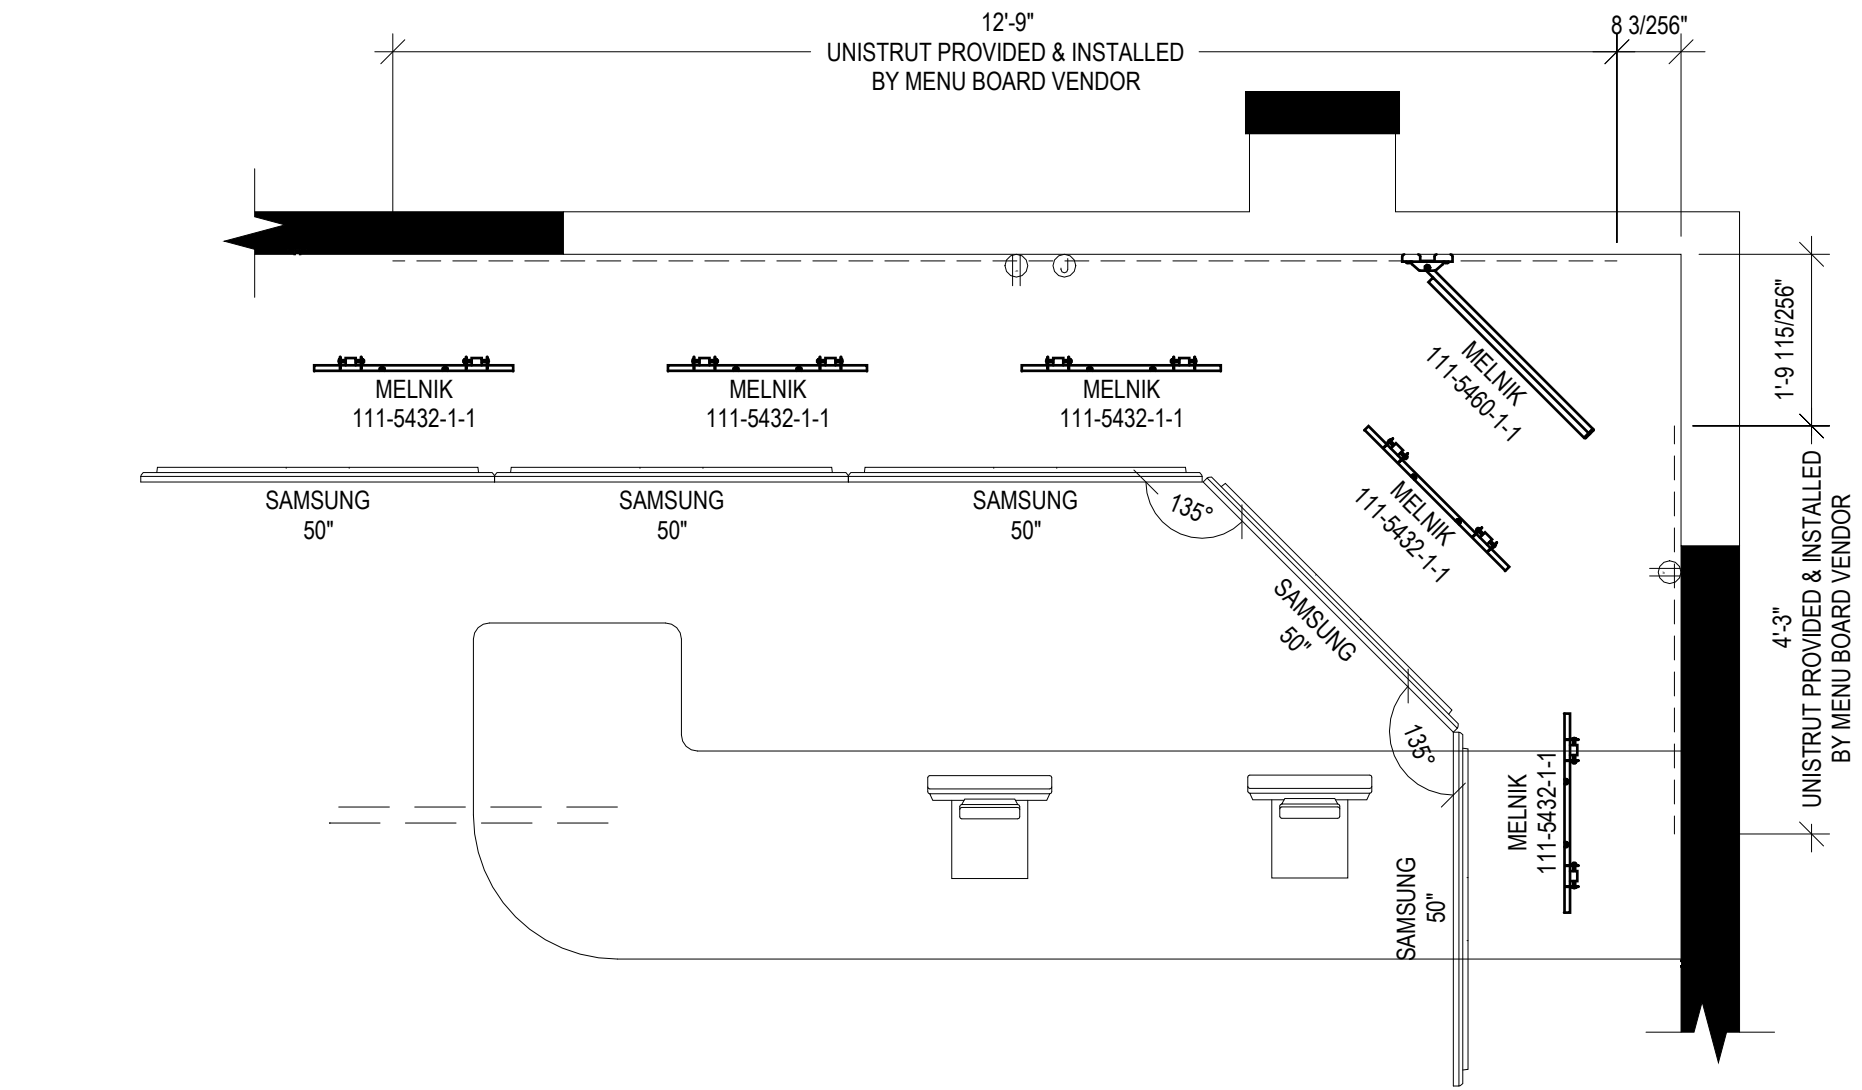
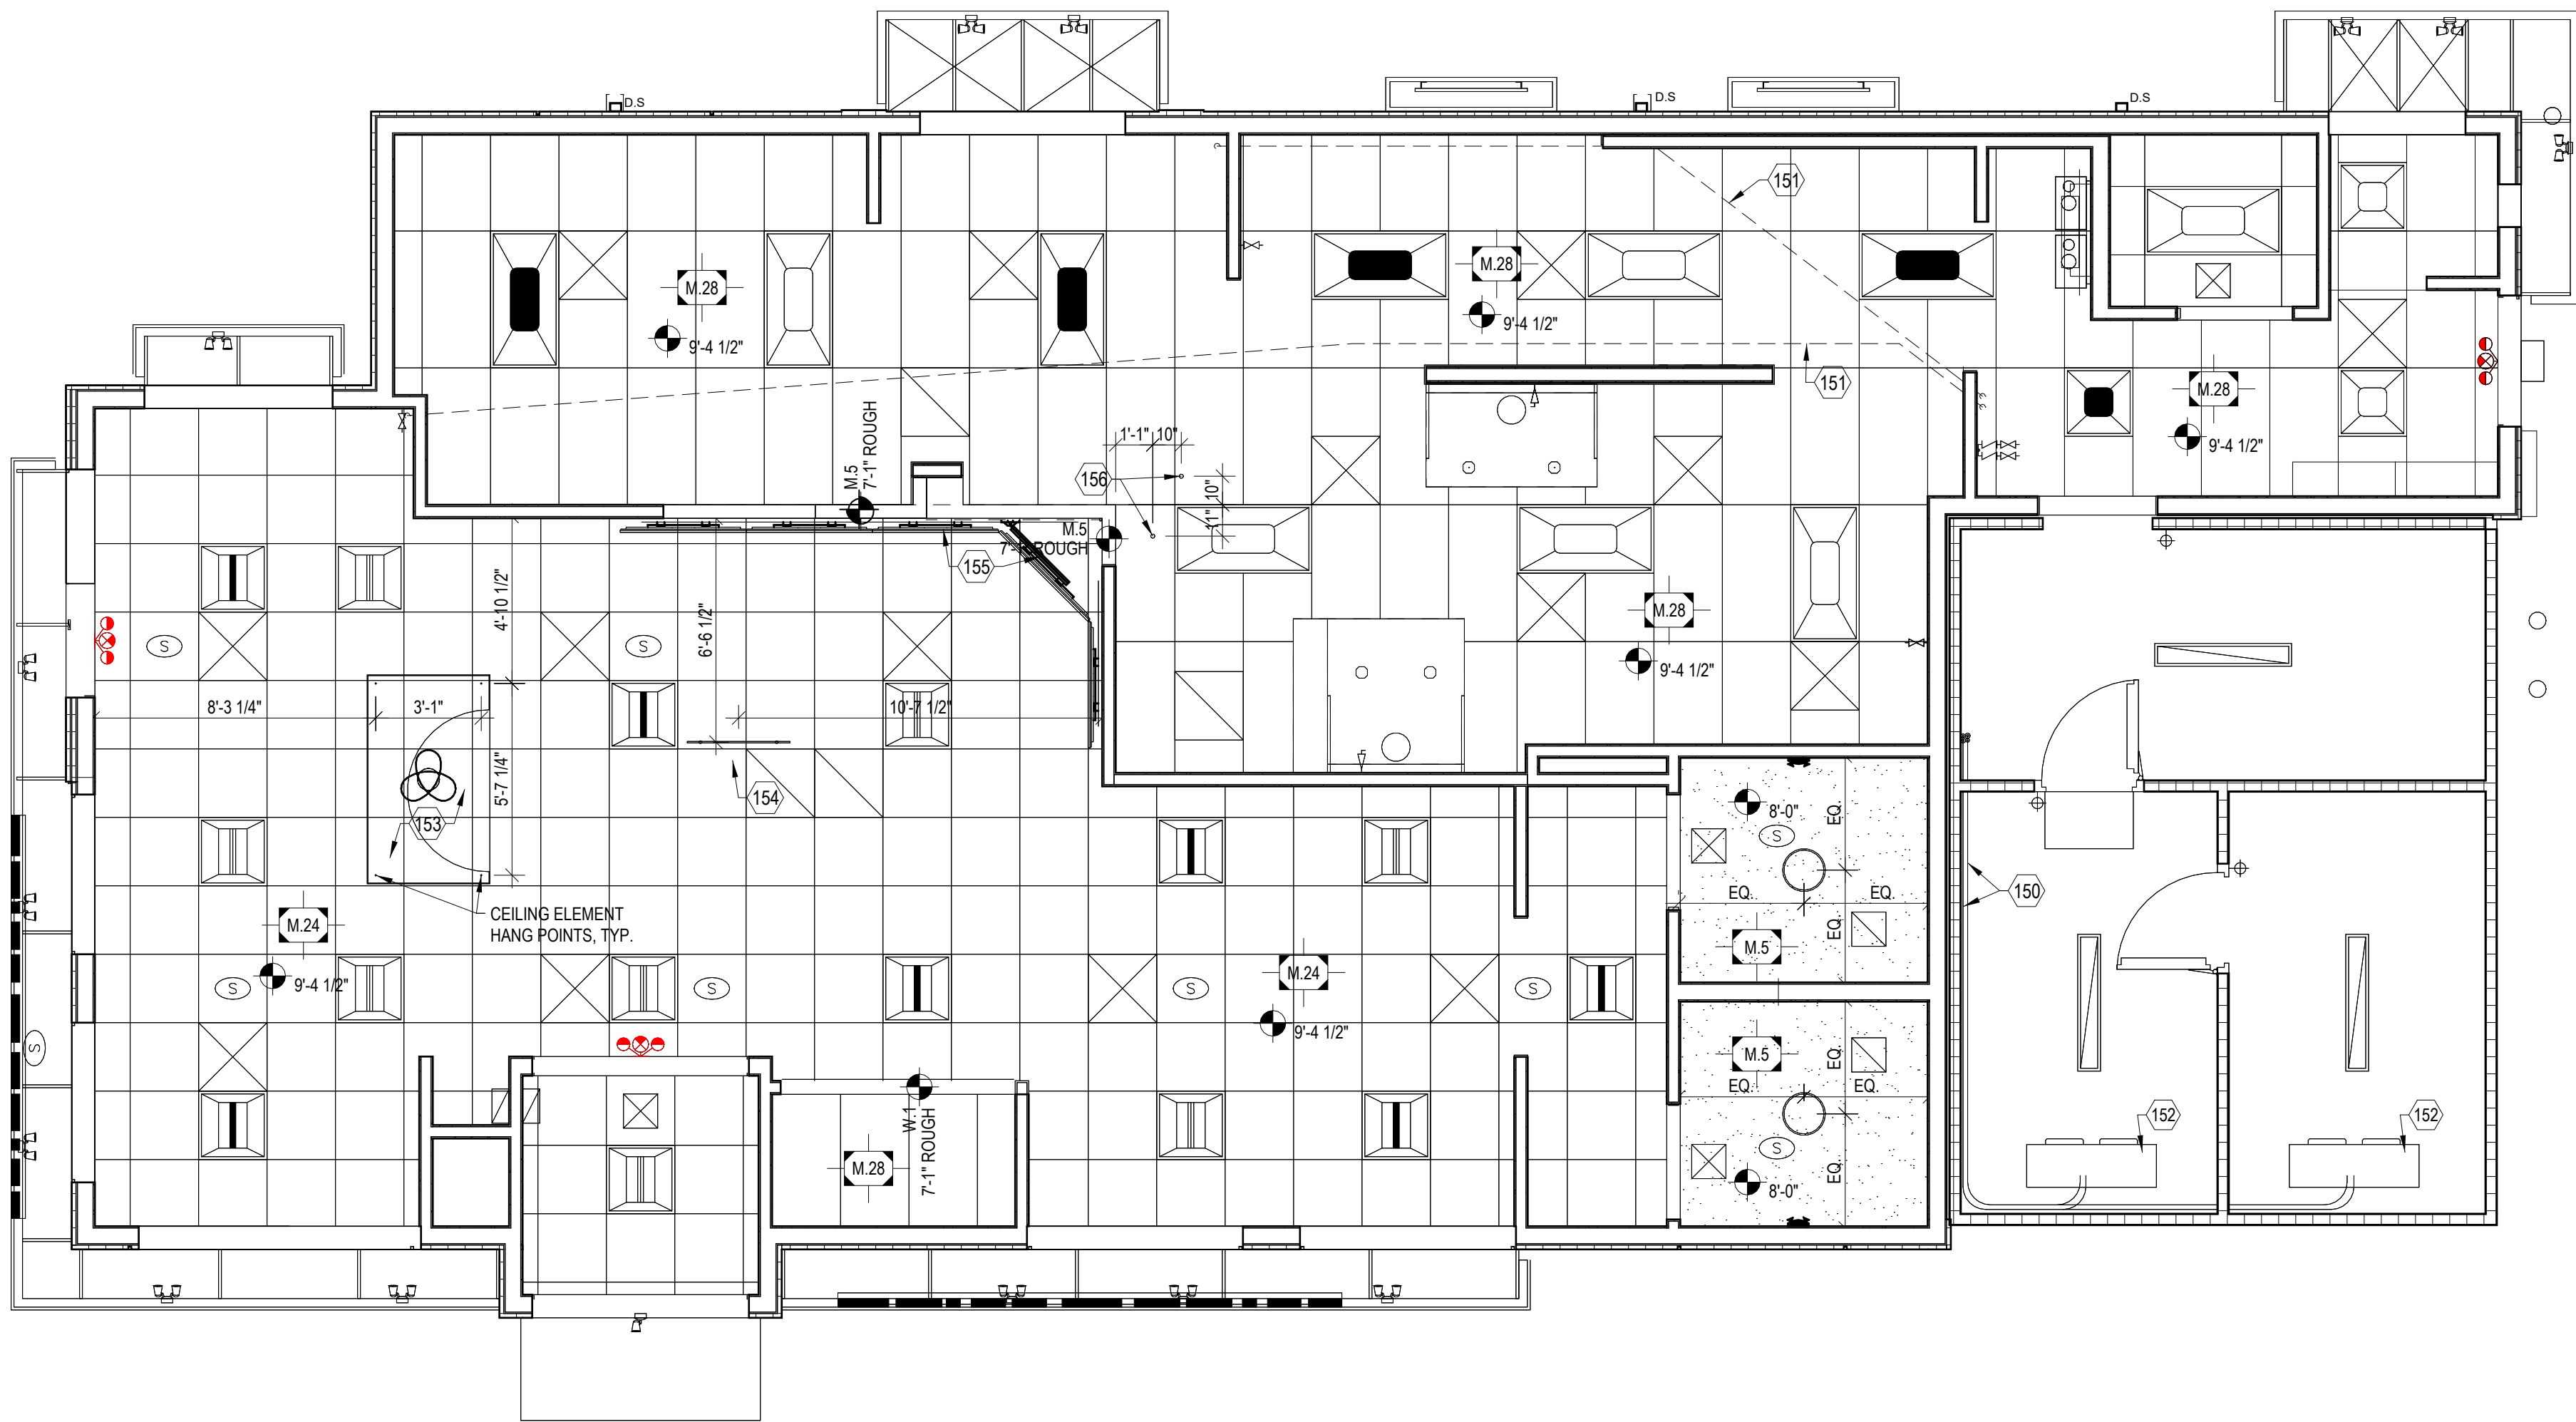


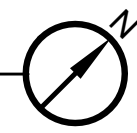

MENU BOARD LAYOUT

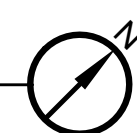

REFLECTED CEILING PLAN

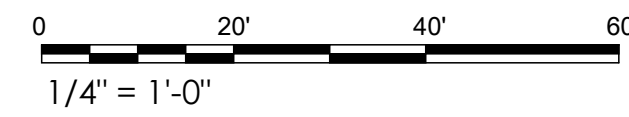

- REFLECTED CEILING PLAN GENERAL NOTES:**
- Ceilings and other suspended items shall be attached to structure by fully embedded or "shear" connection; pull out connections are not acceptable.
 - All gypsum board ceilings shall be 5/8" type 'X' gypsum board on light gauge framing or suspension system.
 - Ceiling and soffit heights noted on Reflected Ceiling Plans, are above finish floor.
 - Center all devices, sprinkler heads, etc. in ceiling tiles.
 - All soffits over casework to extend 1" beyond the face of casework.
 - Provide continuous sound batt insulation above all toilet room ceilings.
 - Fire sprinkler contractor shall reference all drawings and specifications for determining proper coverage and sprinkler head layout/design.
 - Reveal molding to be used at all intersections of different materials. All soffit reveals shall be a continuation of vertical wall reveals.
 - Refer to electrical drawings for location of reused, relocated, existing or new light locations. Patch all GWB ceilings with new gypsum wall board where damaged or removed for new work. Match existing depth, finish and color of ceiling to be patched.
 - Ceiling heights indicated in existing areas are approximate. Maximize where possible. Where ceiling grids are to be extended, match existing height, direction, manufacturer, style, color and type of grid.

- REFLECTED CEILING PLAN - KEYNOTES**
- PRE-CHARGED LINESET MOUNTED/SECURED TO WALK-IN CEILING - REFER TO ROOF PLAN FOR PENETRATION LOCATION AND DETAILS, FERRET TO MANUFACTURER SPECIFICATIONS FOR TYPICAL UTILITY PENETRATION REQUIREMENTS.
 - RUN SYRUP LINE(S) FROM BAF-N-BOX TO DRINK HEAD(S) & MISTY SLUSH. SEE PLUMBING FOR ADDITIONAL NOTES REGARDING OVERHEAD OR UNDERGROUND INSTALLATION.
 - WALK-IN LIGHTING PROVIDED BY MANUFACTURER, INSTALLED BY ELECTRICAL CONTRACTOR.
 - COORDINATE LOCATION OF CEILING ELEMENT AND PENDANT LIGHTS WITH COUNTER HEIGHT SEATING. COORDINATE LOCATION OF MOBILE ORDERS SIGN WITH FRONT COUNTER.
 - DIGITAL MENU BOARDS, MONITORS AND MOUNTING HARDWARE PROVIDED & INSTALLED BY VENDOR, SEE DETAIL 2 INSERT sheet!!
 - POLE MOUNTED KITCHEN MONITOR, MOUNTING HARDWARE PROVIDED BY EPOS VENDOR AND INSTALLED BY G.C.

REFLECTED CEILING PLAN LEGEND

- HEIGHT ABOVE FINISHED FLOOR
- LIGHT FIXTURE (SEE ELECTRICAL)
- LIGHT FIXTURE (SEE ELECTRICAL)
- LIGHT FIXTURE (SEE ELECTRICAL)
- LIGHT FIXTURE (SEE ELECTRICAL)
- LIGHT FIXTURE (SEE ELECTRICAL)
- LIGHT FIXTURE (SEE ELECTRICAL)
- CEILING MOUNTED EMERGENCY EXIT LIGHT (SEE ELEC.)
- EMERGENCY LIGHT FIXTURE (SEE ELEC)
- VCT 2x4 VINYL CEILING TILE
- AC1 2x2 ACOUSTICAL CEILING TILE
- GYP1: GYPSUM BOARD WITH FRAMING.
- 24" X 24" SUPPLY AIR DIFFUSER
- 24" X 24" RETURN AIR GRILLE
- 12" X 12" SUPPLY DIFFUSER



REVISIONS:

DELTA	DESCRIPTION	DATE
-------	-------------	------

DATE OF ISSUE: 04.13.2026

MA PROJECT NO: 0559-25

PROJECT PHASE: CD

DRAWN BY: RP

REFLECTED CEILING PLAN

A-103