



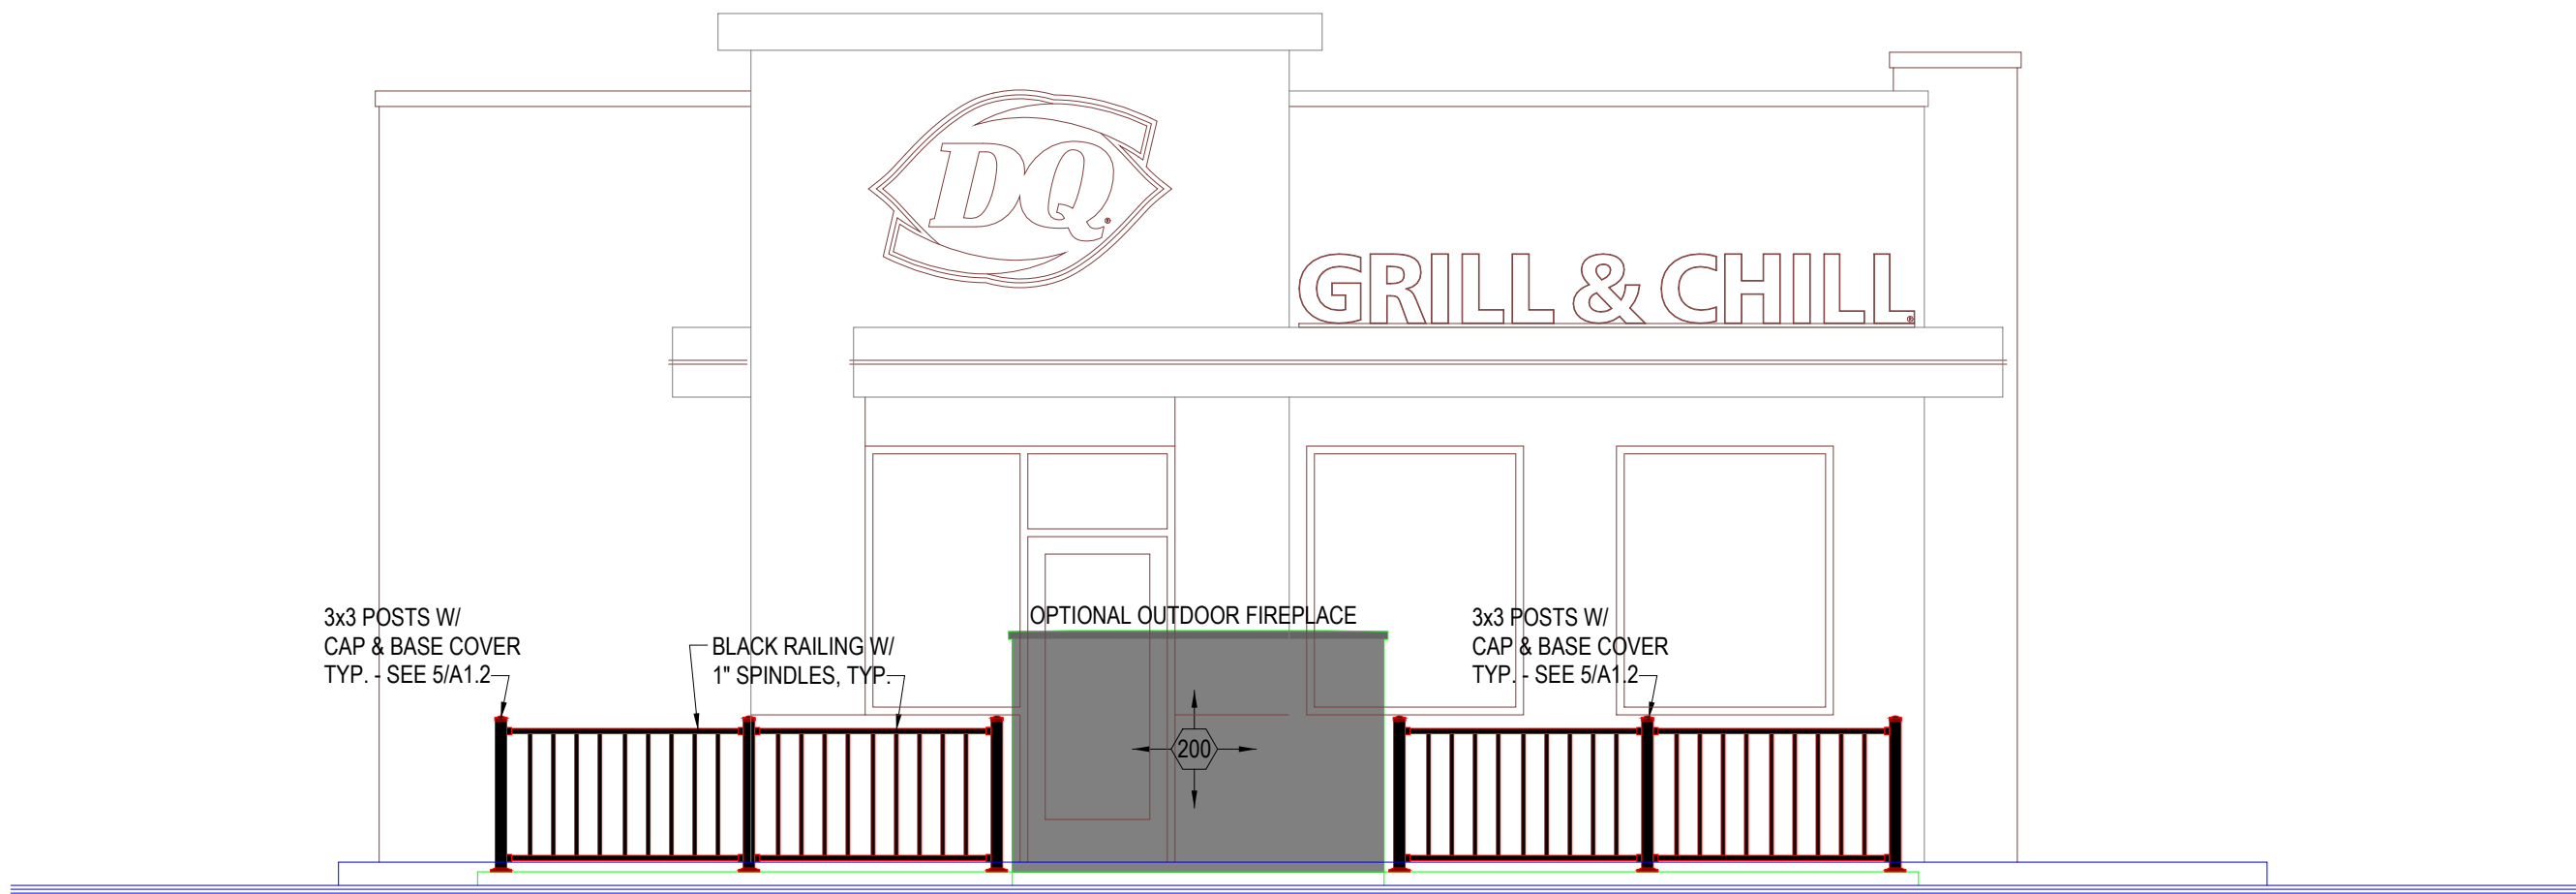


PATIO FRONT ELEVATION

Scale is 1/4" = 1'-0" when printed full size.

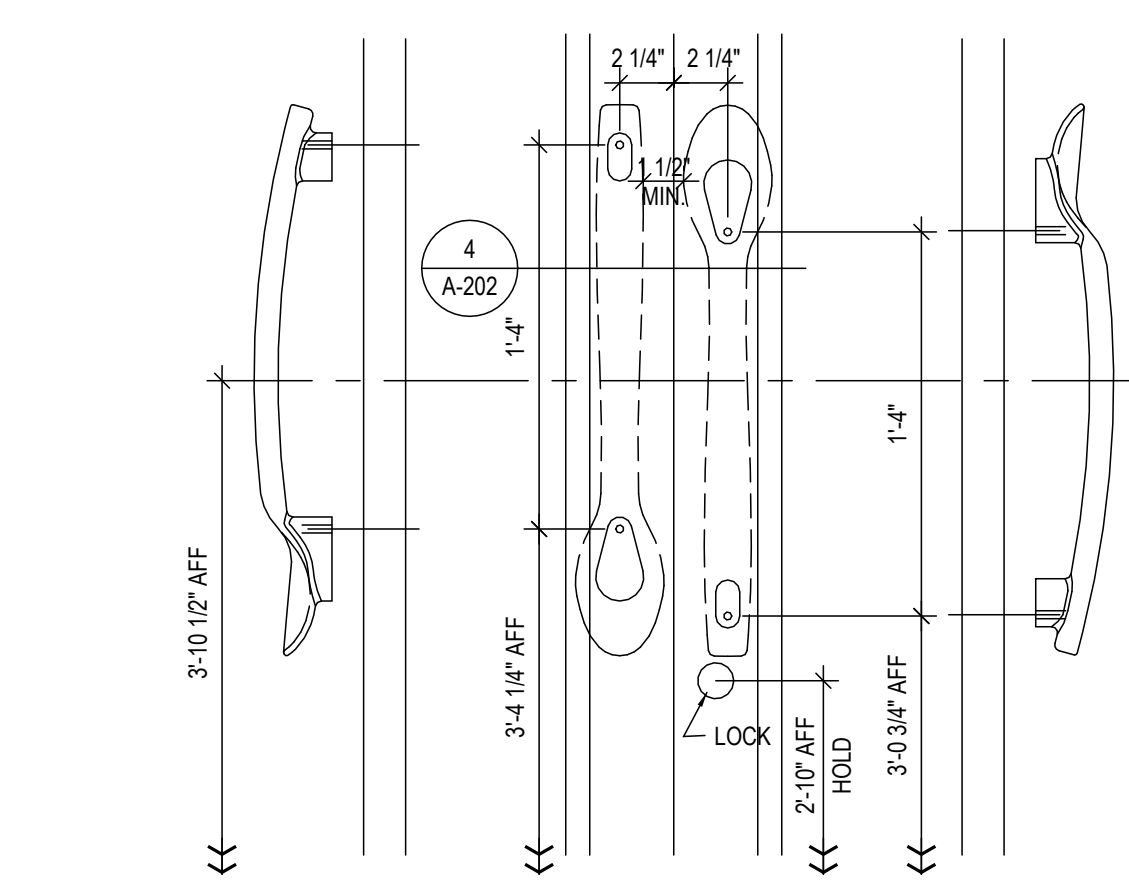

Spoon Handle Detail

1 1/2" = 1'-0"

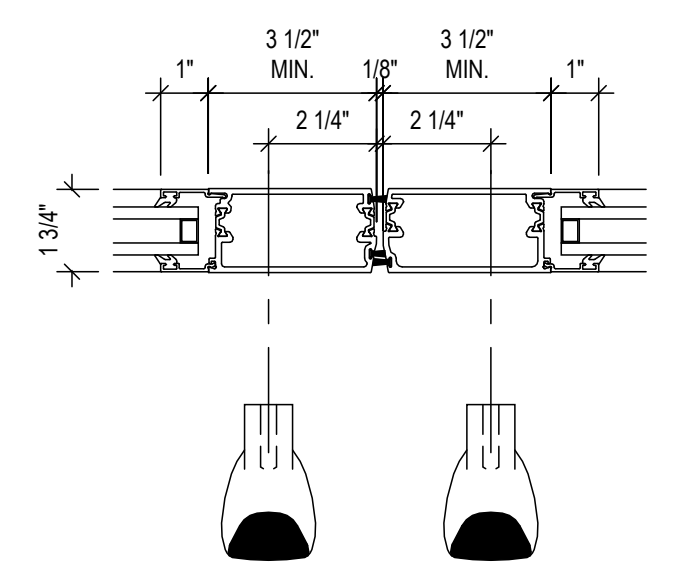

Spoon Handle Detail 2

3" = 1'-0"


OPENING SCHEDULE											
NATIONAL ACCOUNT DOOR AND FRAME SUPPLIER (PLAM, WOOD AND H.M.) HAMILTON PARKER, SEE NATIONAL VENDORS LIST											
OPNG. NO.	OPENING LOCATION	SIZE	FRAME			DOOR			FIRE RATING	HARDWARE GROUP	NOTES:
			TYPE	MATERIAL	FINISH	TYPE	MATERIAL	FINISH			
100A	VESTIBULE (EXT.)	6'-4" x 8'-11 3/8" x 4 1/2"	F-3	ALUM.	CLR	B	ALUM.	CLR	-	E1	SEE 3/3.2 & 4/A3.2 FOR DOOR HANDLE INSTALLATION.
100B	VESTIBULE (EXT.)	6'-4" x 7'-2" x 4 1/2"	F-4	ALUM.	CLR	B	ALUM.	CLR	-	E2	SEE 3/3.2 & 4/A3.2 FOR DOOR HANDLE INSTALLATION.
101A	DINING ROOM	6'-2 3/4" x 6'-3 3/4" x 4 1/2"	F-6	ALUM.	CLR	-	-	-	-	-	-
101B	DINING ROOM	6'-2 3/4" x 6'-3 3/4" x 4 1/2"	F-6	ALUM.	CLR	-	-	-	-	-	-
101C	DINING ROOM	8'-4" x 5'-9 3/8" x 4 1/2"	F-7	ALUM.	CLR	-	-	-	-	-	-
101D	DINING ROOM	4'-8" x 5'-9 3/8" x 4 1/2"	F-7	ALUM.	CLR	-	-	-	-	-	-
101E	DINING ROOM	4'-8" x 5'-9 3/8" x 4 1/2"	F-6	ALUM.	CLR	-	-	-	-	-	-
101F	DINING ROOM	6'-8" x 8'-11 3/8" x 4 1/2"	F-8	ALUM.	CLR	B	-	-	-	-	-
101G	DINING ROOM	5'-6" x 5'-9 3/8" x 4 1/2"	F-6	ALUM.	CLR	-	-	-	-	-	-
102	RESTROOM	3'-4" x 7'-2" x 5 3/4"	F-1	HM.	PNT	A	PC	-	-	R1	UNDERCUT BY 1" - PLAM. WILSONART NORTH SEA D90-60.
103	RESTROOM	3'-4" x 7'-2" x 5 3/4"	F-1	HM.	PNT	A	PC	-	-	R1	UNDERCUT BY 1" - PLAM. WILSONART NORTH SEA D90-60.
105	DRIVE-THRU	6'-0" x 5'-4" x 4 1/2"	F-5	ALUM.	CLR	-	-	-	-	-	-
109	OFFICE	3'-4" x 7'-2" x 5 3/4"	F-1	HM.	PNT	A	PC	-	-	O2	UNDERCUT BY 1" - PLAM. WILSONART NORTH SEA D90-60.
110	SERVICE	3'-10" x 7'-2" x 5 3/4"	F-1	HM.	PNT	A	HM	-	-	S1	-
111A	DRIVE-THRU	4'-0" x 5'-4" x 4 1/2"	F-9	ALUM.	CLR	-	-	-	-	-	-
111B	DRIVE-THRU	1'-3" x 4'-0" x 4 1/2"	F-10	ALUM.	CLR	-	-	-	-	-	-

NOTES:
1. PARTICLE CORE DOORS, SIZE AS PER PLAN AND SCHEDULE. ALL EDGES/SURFACES TO BE COVERED WITH PLASTIC BANNING/HOLLOW METAL DOOR(S). SIZE AS PER PLAN AND SCHEDULE. (HOT ROLLED LEVEL 2 MODEL 2) STEEL TO BE 18 GA. INTERIOR TO BE FOAM INSULATION, WITH INTEGRAL REINFORCEMENT FOR CLOSURE AND PANIC HARDWARE (TYPICAL AT ALL). CLEAR, 1" INSULATED, LOW E.

HARDWARE GROUPS

NATIONAL ACCOUNT DOOR AND FRAME SUPPLIER (PLAM, WOOD AND H.M.) HAMILTON PARKER, SEE NATIONAL VENDORS LIST
NOTE: THIS IS A PROTOTYPICAL SCHEDULE. ALL GROUPS MAY NOT BE USED.

GROUP #E1: TYPICAL EXTERIOR VESTIBULE DOORS - CLOSER: HAGER MFG., MODEL #5200, ALM. - HINGES: HAGER MFG., ECB1199, US320, WITH NON-REMOVABLE PINS, 4.5"x4.5", (4) HINGES PER LEAF. - KEYED CYLINDERS: HAGER MFG., 3902 MORTISE CYLINDER, US260, PROVIDE (2) KEYS PER DOOR, ALL CYLINDERS KEYPED ALIKE. (MOUNTED AT 34" AFF, COORDINATE W/ SPOON HANDLE). - MORTISE DEADLOCK: HAGER MFG., 3800, US260 - SPOON HANDLE (PROVIDED & INSTALLED BY ALUM. STOREFRONT CONTRACTOR, AVAILABLE FROM HJC. SEE ADD NATIONAL VENDORS LIST) - PUSH BAR: HAGER MFG., 130S, 32D - SWEEP: HAGER MFG., 801S, MIL ALUM FINISH, SIZED TO FIT DOOR - THRESHOLD: HAGER MFG., 412 S, MIL ALUM FINISH, SIZED TO FIT DOOR OPENING WIDTH. - WEATHERSTRIPPING: HAGER MFG., 891S, MIL ALUM FINISH, SIZED TO FIT DOOR.	GROUP #E3: TYPICAL EXTERIOR PATIO/GRESS DOOR - CLOSER: HAGER MFG., MODEL #5200, ALM. - HINGES: HAGER MFG., ECB1199, US320, WITH NON-REMOVABLE PINS, 4.5"x4.5", (4) HINGES PER LEAF. - KEYED CYLINDERS: HAGER MFG., 3902 MORTISE CYLINDER, US260, PROVIDE (2) KEYS PER DOOR, ALL CYLINDERS KEYPED ALIKE. (MOUNTED AT 34" AFF, COORDINATE W/ SPOON HANDLE) - MORTISE DEADLOCK: HAGER MFG., 3800, US260 - SPOON HANDLE (PROVIDED & INSTALLED BY ALUM. STOREFRONT CONTRACTOR, AVAILABLE FROM HJC. SEE ADD NATIONAL VENDORS LIST) - PUSH BAR: HAGER MFG., 130S, 32D - SWEEP: HAGER MFG., 801S, MIL ALUM FINISH, SIZED TO FIT DOOR - THRESHOLD: HAGER MFG., 412 S, MIL ALUM FINISH, SIZED TO FIT DOOR OPENING WIDTH. - WEATHERSTRIPPING: HAGER MFG., 891S, MIL ALUM FINISH, SIZED TO FIT DOOR.	GROUP #S1: TYPICAL REAR SERVICE DOOR - CLOSER: HAGER MFG., MODEL #5200, ALM. - EXIT DEVICE: HAGER MFG., 4701, ALM - HINGES: HAGER MFG., ECB1199, US260, WITH NON-REMOVABLE PINS, 4.5"x4.5", (4) HINGES PER LEAF. - KICK PLATE: HAGER MFG., 190S - 34"W X 20"H, INSTALLED ON PUSH SIDE - PROTECTOR, TRIM: HAGER, MFG., MDL #H02250, US320 - PULL HAGER MFG., 47NL, 32D, EXTERIOR SIDE OF DOOR - SWEEP: HAGER MFG., 891S, MIL ALUM FINISH, SIZED TO FIT DOOR - THRESHOLD: HAGER MFG., 412 S, MIL ALUM FINISH, SIZED TO FIT DOOR OPENING WIDTH. - DOOR VIEWER: HAGER MFG., 1756, US260, FACTORY INSTALLED - WEATHERSTRIPPING: HAGER MFG., 891S, MIL ALUM FINISH, SIZED TO FIT DOOR. - EXIT ALARM: DETEX, EAX-600W BATTERY POWERED DOOR MOUNTED WEATHERIZED EXIT - DOOR SILENCERS: HAGER MFG., 307D
GROUP #E2: TYPICAL INTERIOR VESTIBULE DOORS - CLOSER: HAGER MFG., MODEL #5200, ALM. - HINGES: HAGER MFG., ECB1199, US320, WITH NON-REMOVABLE PINS, 4.5"x4.5", (4) HINGES PER LEAF. - PUSH/PULL BAR: HAGER MFG., 1590 LH COMBO, & 1590 RH COMBO, US320 - DOOR STOP: HAGER MFG., 241F US260, (1) PER LEAF	GROUP #R1: TYPICAL SINGLE OCCUPANT RESTROOM DOOR - CLOSER: HAGER MFG., MODEL #5200, ALM. - HINGES: HAGER MFG., ECB1199, US260, WITH NON-REMOVABLE PINS, 4.5"x4.5", (3) HINGES PER LEAF. - KICK PLATE: HAGER MFG., 190S - 34"W X 10"H, INSTALLED ON PUSH SIDE - CONVEX DOOR STOP: HAGER MFG., #232W, US320 - PUSH PLATE: HAGER MFG., 30S, 4"x16", INSTALLED ON PUSH SIDE - PULL HANDLE: HAGER MFG., 103E, 4"x16", US260 - FOOT OPERATED DOOR PULL: HAGER MFG., 190F, US320 - DOOR SILENCERS: HAGER MFG., 307D	GROUP #R2: TYPICAL RESTROOM DOOR - CLOSER: HAGER MFG., MODEL #5200, ALM. - HINGES: HAGER MFG., ECB1199, US260, WITH NON-REMOVABLE PINS, 4.5"x4.5", (3) HINGES PER LEAF. - KICK PLATE: HAGER MFG., 190S - 34"W X 10"H, INSTALLED ON PUSH SIDE - CONVEX DOOR STOP: HAGER MFG., #232W, US320 - PUSH PLATE: HAGER MFG., 30S, 4"x16", INSTALLED ON PUSH SIDE - PULL HANDLE: HAGER MFG., 103E, 4"x16", US260 - FOOT OPERATED DOOR PULL: HAGER MFG., 190F, US320 - DOOR SILENCERS: HAGER MFG., 307D

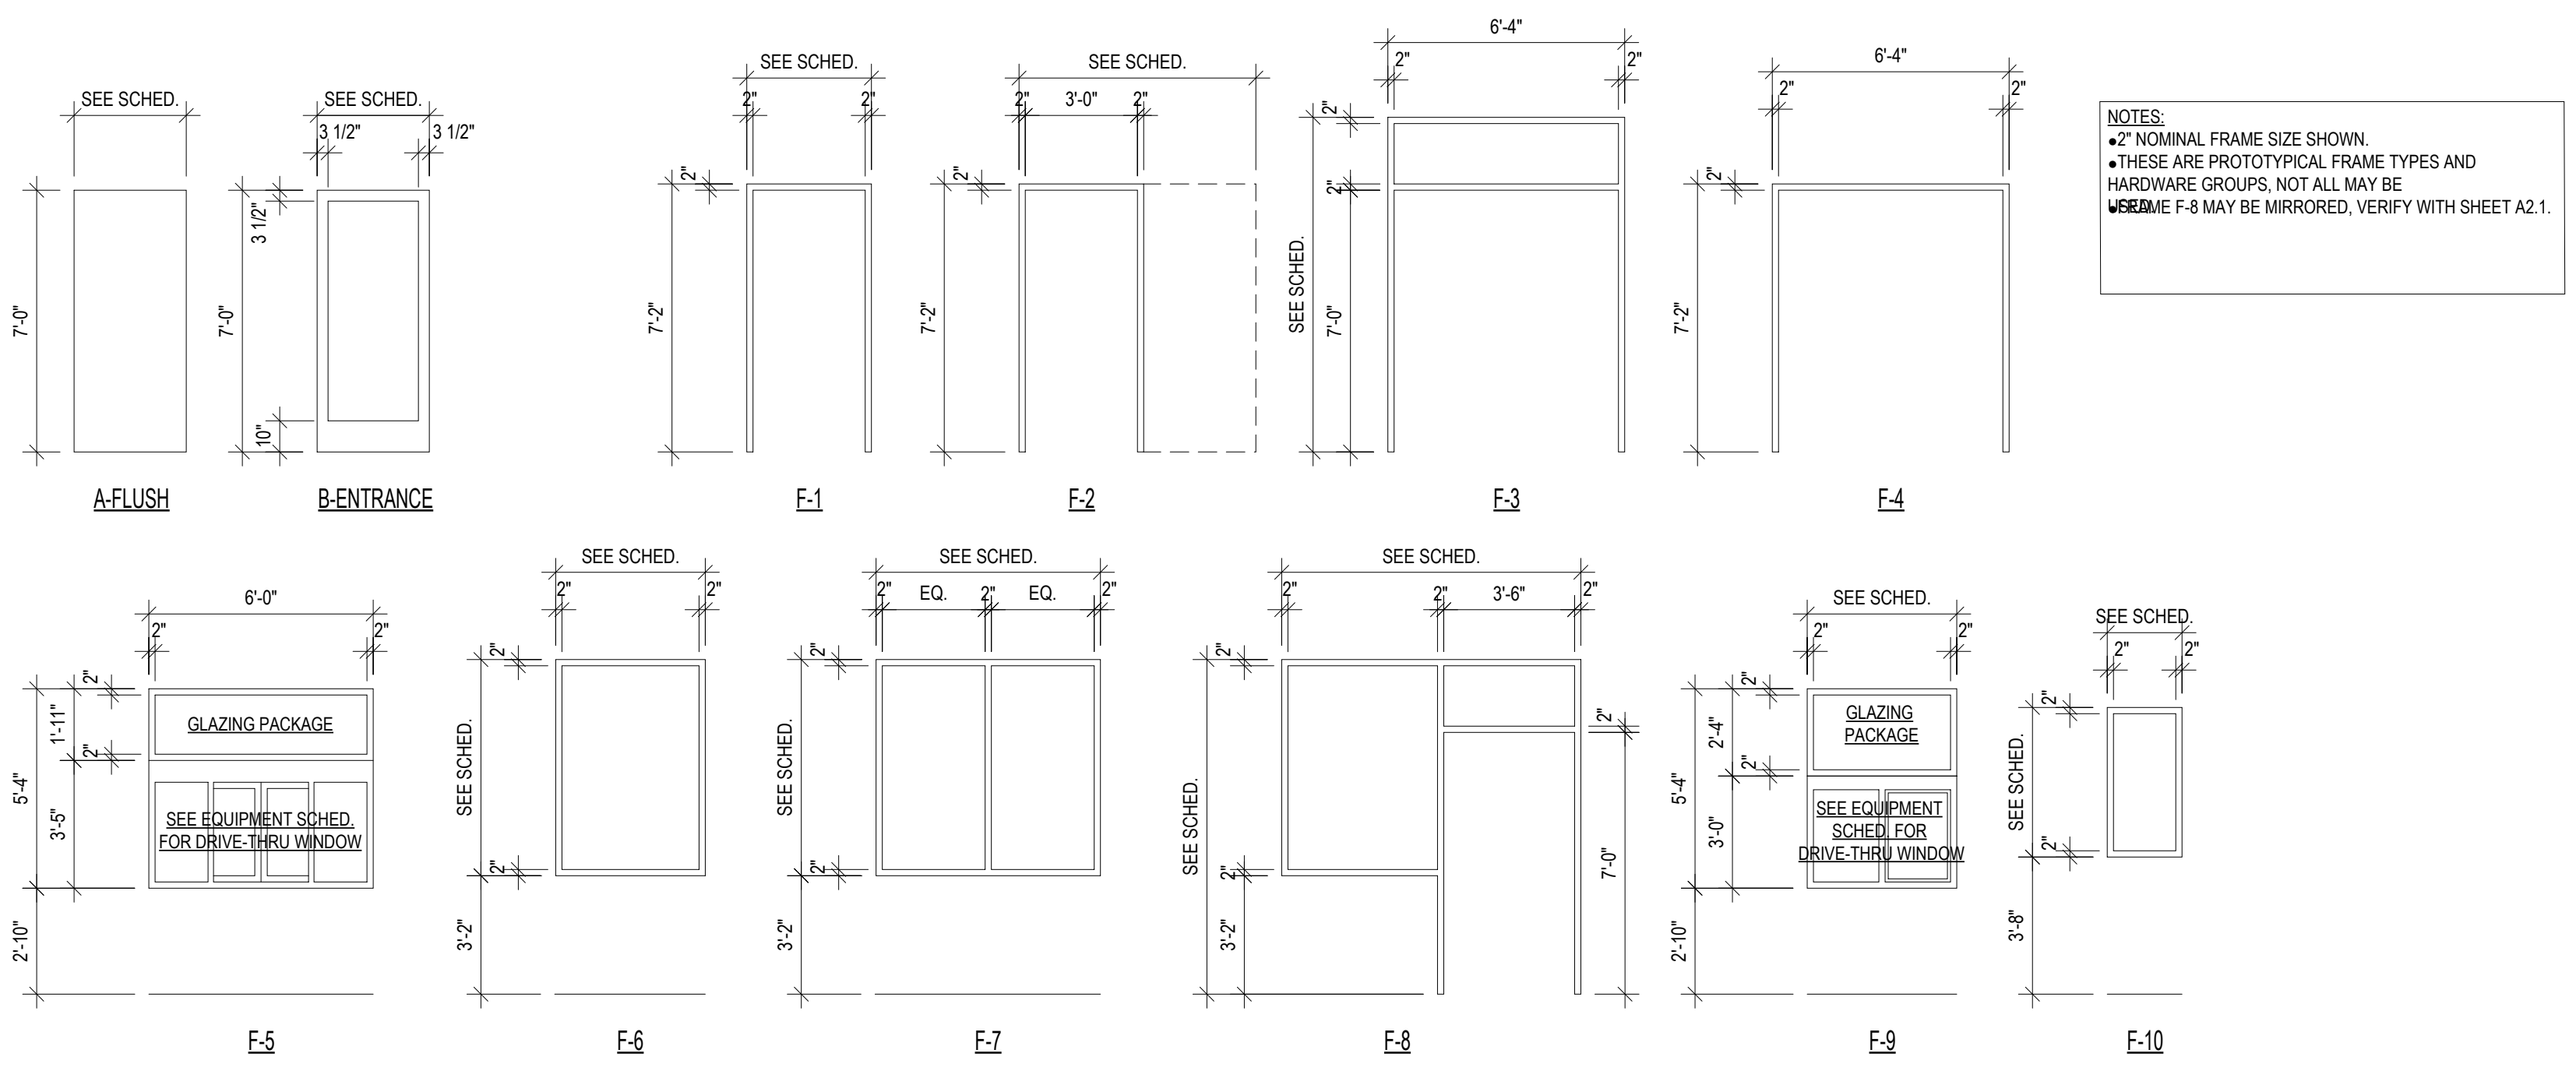

Door & Window Frames

Scale is 1/4" = 1'-0" when printed full size.

BUILDING ELEVATION - KEYNOTES

- STONE: MFR: BORAL STONE PRODUCTS LLC. STYLE: PRG-FIT LEDGESTONE, DRY STACK. COLOR: PLATINUM. NOTE: CAPSTONE: ELDERADO STONE - CHISELED EDGE COLUMN CAP, COLOR: SMOKE
- EIFS: (LIGHT). MFR: STO CORPORATION. COLOR: NA19-0021(MATCHES BENJAMIN MOORE, TEMPORAL SPIRIT 965). FINISH: 310 STO (FINE SAND). NOTE: PROVIDE HIGH-IMPACT EIFS FROM GRADE TO 3'-0" A.F.F.. LRV: 64
- EIFS: (RED). MFR: STO CORPORATION. COLOR: NA19-0022(MATCHES BENJAMIN MOORE, CALENTE AF-290). FINISH: 130D STOUT 1.00 (FINE SAND). NOTE: PROVIDE HIGH IMPACT EIFS FROM GRADE TO 3'-0" A.F.F.. LRV: 7.
- EIFS: (DARK). MFR: STO CORPORATION. COLOR: NA19-0023(MATCHES BENJAMIN MOORE, DEEP CREEK 1477). FINISH: 130D STOUT 1.00 (FINE SAND). NOTE: PROVIDE HIGH IMPACT EIFS FROM GRADE TO 3'-0" A.F.F.. LRV: 13
- COPING & SCUPPERS: MFR: HOLCIM (FORMERLY FIRESTONE UNA-CLAD). MATL: 24 GA. STEEL. COLOR: SILVER METALLIC. FINISH: KYNAR 500. VENDOR: ARCHITECTURAL METALS, SEE NATIONAL VENDORS LIST.
- PAINT PATIO RAILING, LIGHTS, PERGOLA COLUMNS: MFR: BENJAMIN MOORE. COLOR: P28 COBBLESTONE PATH 1606. PRODUCT: ULTRA SPEC HP DTM ACRYLIC SEMI-GLOSS ENAMEL. HP28. PRIMER: ULTRA SPEC HP DTM ACRYLIC METAL PRIMER HP04.
- METAL PANEL: MFR: ALPOLIC. STYLE: 4MM. COLOR: SHIMMER DQS MAROON GOLD. NOTE: MUST BE INSTALLED HORIZONTALLY. REFERENCE ARROWS ON BACK OF PANEL MUST BE ALIGNED IN THE SAME DIRECTION. VENDOR: ARCHITECTURAL METALS, SEE NATIONAL VENDORS LIST.
- METAL EYEBROW, OUTRIGGERS, & FLASHINGS: MFR: HOLCIM(FORMERLY FIRESTONE UNA-CLAD). MATL: .040 ALUMINUM. COLOR: EXTRA DARK BRONZE. FINISH: KYNAR 500. VENDOR: ARCHITECTURAL METALS, SEE NATIONAL VENDORS LIST.
- EIFS: (BLUE). MFR: STO CORPORATION. COLOR: NA19-0024 (MATCHES BENJAMIN MOORE, BIG COUNTRY BLUE #2066-30). FINISH: 130D STOUT 1.0 (FINE SAND). NOTE: PROVIDE HIGH IMPACT EIFS FROM GRADE TO 3'-0" A.F.F.. LRV: 16
- STOREFRONT: STYLE: 2" x 4 1/2". FINISH: CLEAR ANODIZED. GLAZING: CLEAR, 1" INSULATED, LOW E.
- EIFS: (ANODIZED). MFR: STO CORPORATION. COLOR: NA20-0019 (MATCHES BENJAMIN MOORE, WILLOW CREEK #468). FINISH: 310 STO (FINE SAND). NOTE: PROVIDE HIGH IMPACT EIFS FROM GRADE TO 3'-0" A.F.F.. LRV: 16
- CORRUGATED METAL: MFR: METAL SALES MANUFACTURING CORPORATION. MATL: 7/8" CORRUGATED 24 GA. STEEL. COLOR: ACRYLIC COATED GALVALUME. VENDOR: ARCHITECTURAL METALS, SEE NATIONAL VENDORS LIST.
- PAINT: MFR: BANIAMM MOORE. COLOR: TEMPORAL SPIRIT 965. PRODUCT: COROTEC COMMAND WATERBORNE ACRYLIC URETHANE SATIN (V392). PRIMER: ON FERROUS METAL COROTEC PREP ALL UNIVERSAL METAL PRIMER(V332).
- TRASH ENCLOSURE SOLID COLOR STAIN: MFR: BENJAMIN MOORE. COLOR: DEEP CREEK 1477. PRODUCT: ARBORCOAT WATERBORNE SOLID DECK & SIDING STAIN #640. PRIMER: SELF PRIMING ON MOST SURFACES (SEE TECH. DATA SHEET FOR DETAILS).
- TRASH ENCLOSURE PAINT: MFR: BENJAMIN MOORE. COLOR: DEEP CREEK 1477. PRODUCT: COROTEC COMMAND WATERBOURNE ACRYLIC URETHANE SATIN (V392). PRIMER: FIRST COAT OF USTED PRODUCT.
- METAL PANEL: MFR: APOLIC. STYLE: 3MM. COLOR: TBX SILVER. NOTE: MUST BE INSTALLED HORIZONTALLY. REFERENCE ARROWS ON BACK OF PANEL MUST BE ALIGNED IN THE SAME DIRECTION. VENDOR: ARCHITECTURAL METALS, SEE NATIONAL VENDORS LIST.
- AWNING: MFR: SUNBRELLA. COLOR: FIRESIST GREY 82030. VENDOR: SIGN SOURCE.
- WELCOME LETTERS: MFR: INDIGO SIGNS. SRIES: DQ SCRIPT (RED "WELCOME"). NOTE: COORDINATE WITH ARCHITECTURAL METALS VENDOR.
- PERGOLA SOLID COLOR STAIN: MFR: BENJAMIN MOORE. COLOR: COBBLESTONE PATH 1606. PRODUCT: ARBORCOAT WATERBORNE SOLID DECK & SIDING STAIN #640. PRIMER: SELF PRIMING ON MOST SURFACES (SEE TECH. DATA SHEET FOR DETAILS).
- WALKIN COOLER/FREEZER: MFR: KOLPAK. COLOR: FACTORY FINISH. VENDOR: WASSERSTROM. NOTE: SEE EQUIPMENT SCHEDULE FOR DETAILS.



REVISIONS:		
DELTA	DESCRIPTION	DATE

DATE OF ISSUE: 04.13.2026

MA PROJECT NO: 0559-25

PROJECT PHASE: CD

DRAWN BY: Author