



BUILDING SECTION GENERAL NOTES

- A. Suspended materials shall be attached to structure with tested connectors for tension or shear condition at frequency to support load applied.
- B. Insulation shall be continuous at the roof plane and shall lap wall insulation.
- C. Route all plumbing, fire sprinkler, mechanical, electrical, fire alarm, piping, and conduit in concealed or furred area only. Exposed piping and conduit shall not be allowed in any area except at electrical and fire riser rooms.

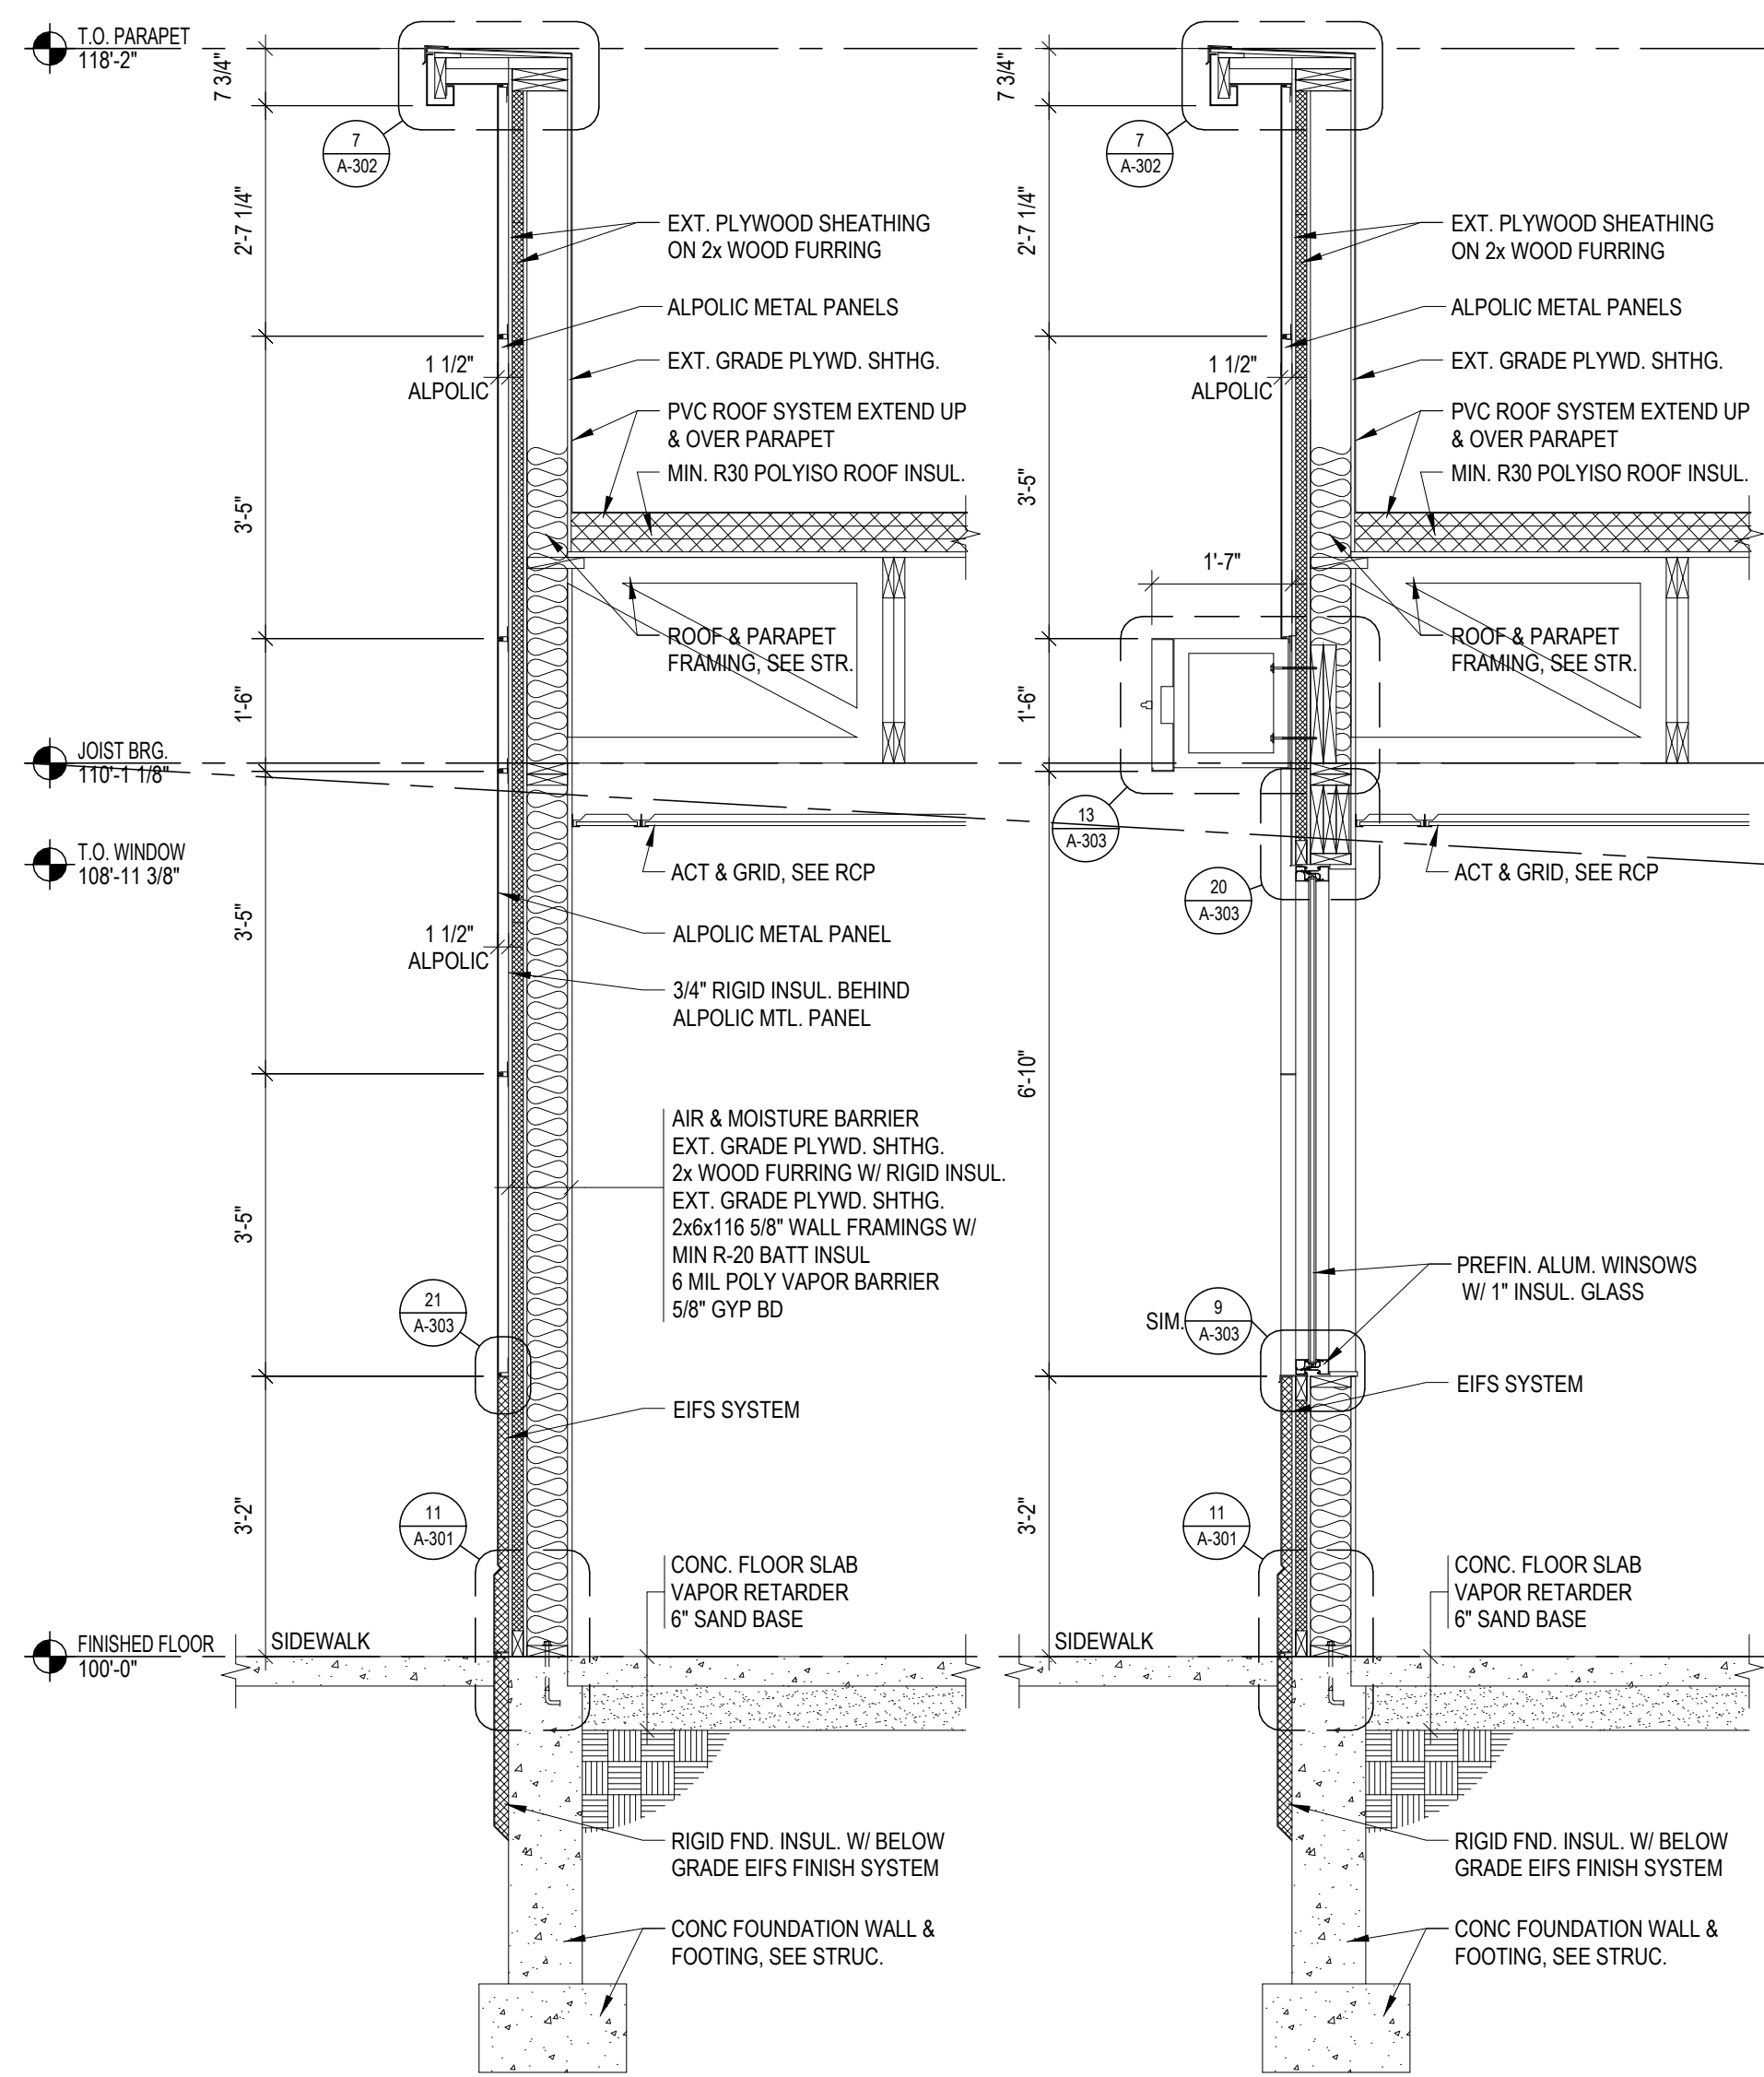

1 SECTION
A-303 SCALE: 1/2" = 1'-0"

2 SECTION
A-303 SCALE: 1/2" = 1'-0"

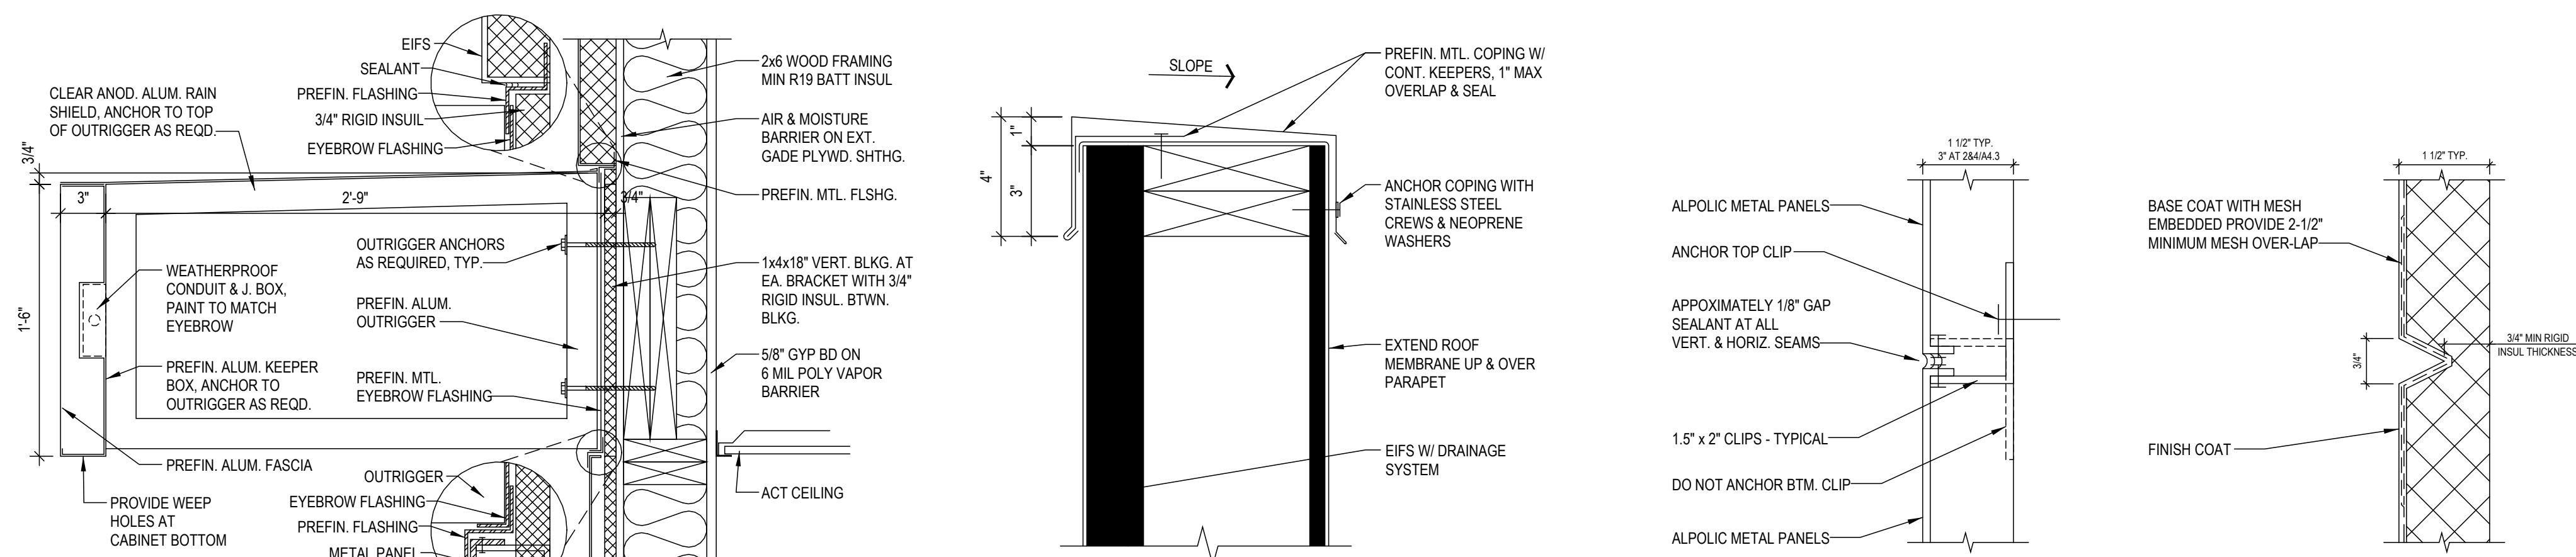


3/4" RIGID INSUL-
DT CANOPY DETAIL
3
A-303 SCALE: 1 1/2" = 1'-0"


4 CAP FLASHING DETAIL
A-303 SCALE: 3" = 1'-0"

5 ALPOLIC PANEL JOINT
A-303 SCALE: 6" = 1'-0"

EIFS REVEAL DETAIL

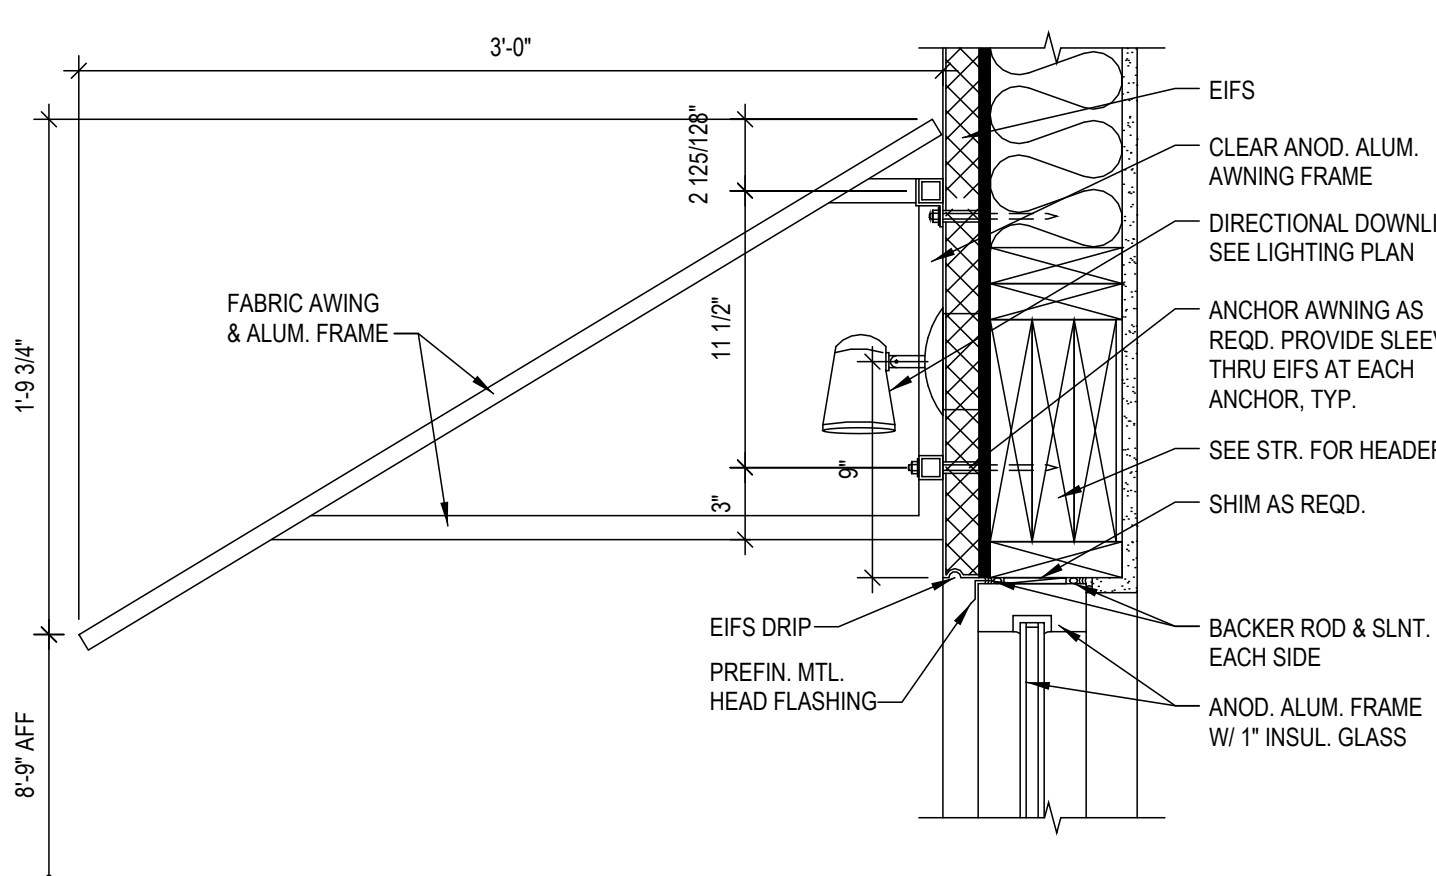


6 ENTRY CANOPY DETAIL
A-303 SCALE: 1 1/2" = 1'-0"

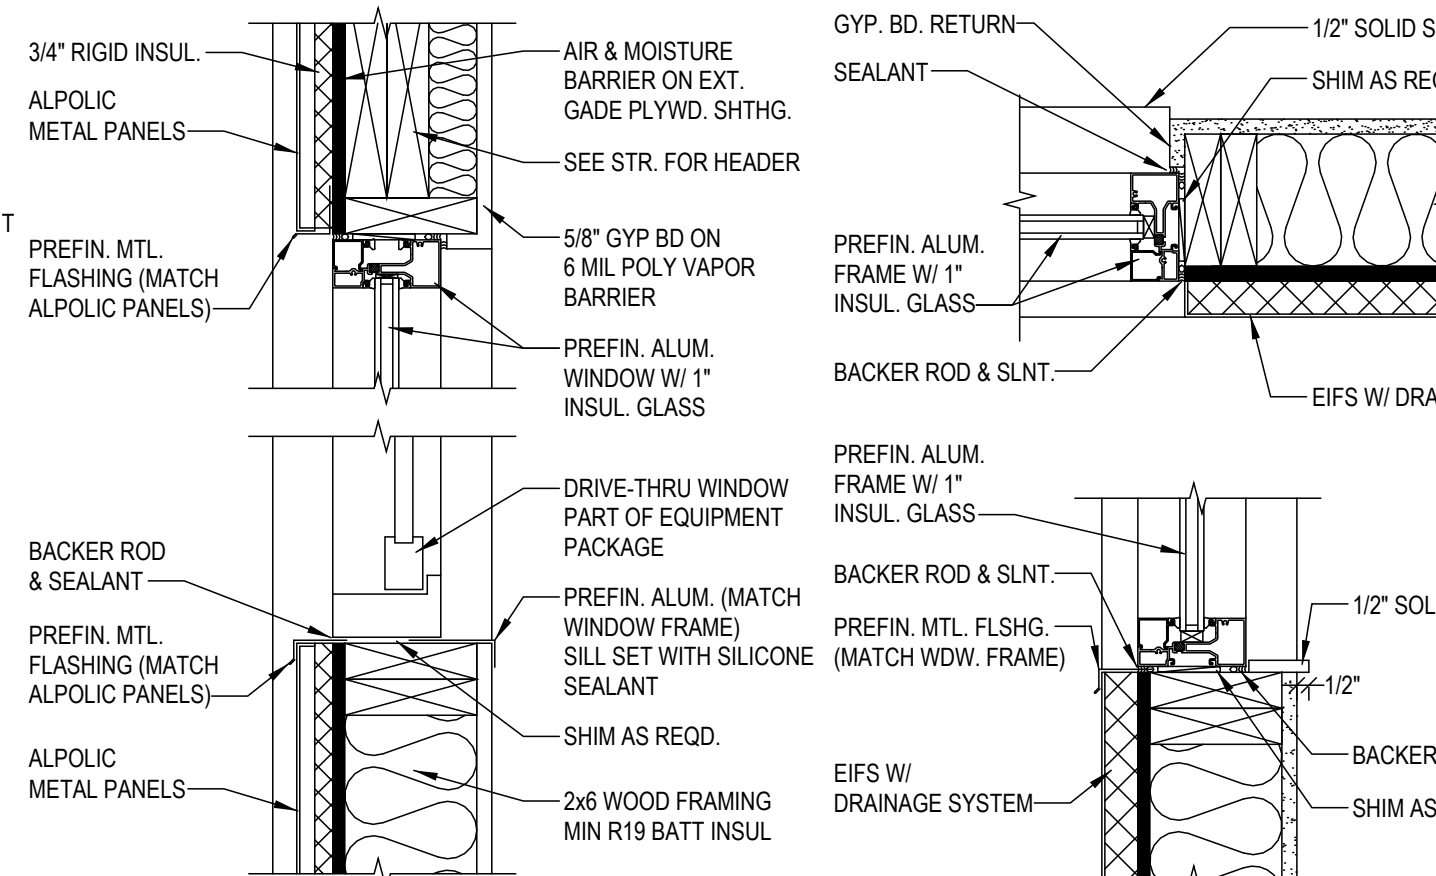


8 DT WINDOW DETAIL
A-303 SCALE: 1 1/2" = 1'-0"

9 WINDOW DETAILS
A-303 SCALE: 1 1/2" = 1'-0"

10 H.M. DOOR DETAIL
A-303 SCALE: 1 1/2" = 1'-0"


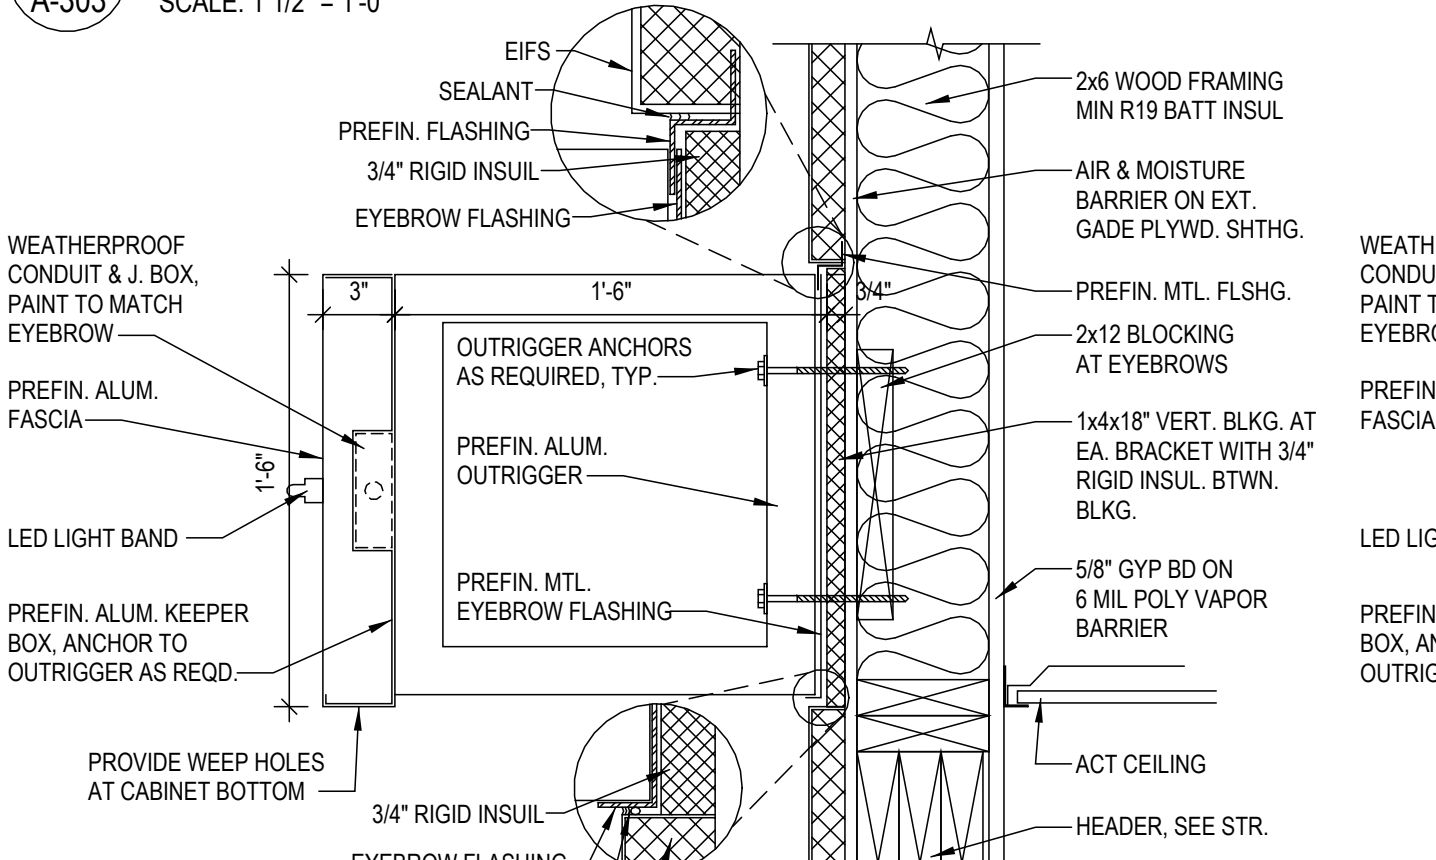


11 EYEBROW DETAIL-EIFS
A-303 SCALE: 1 1/2" = 1'-0"

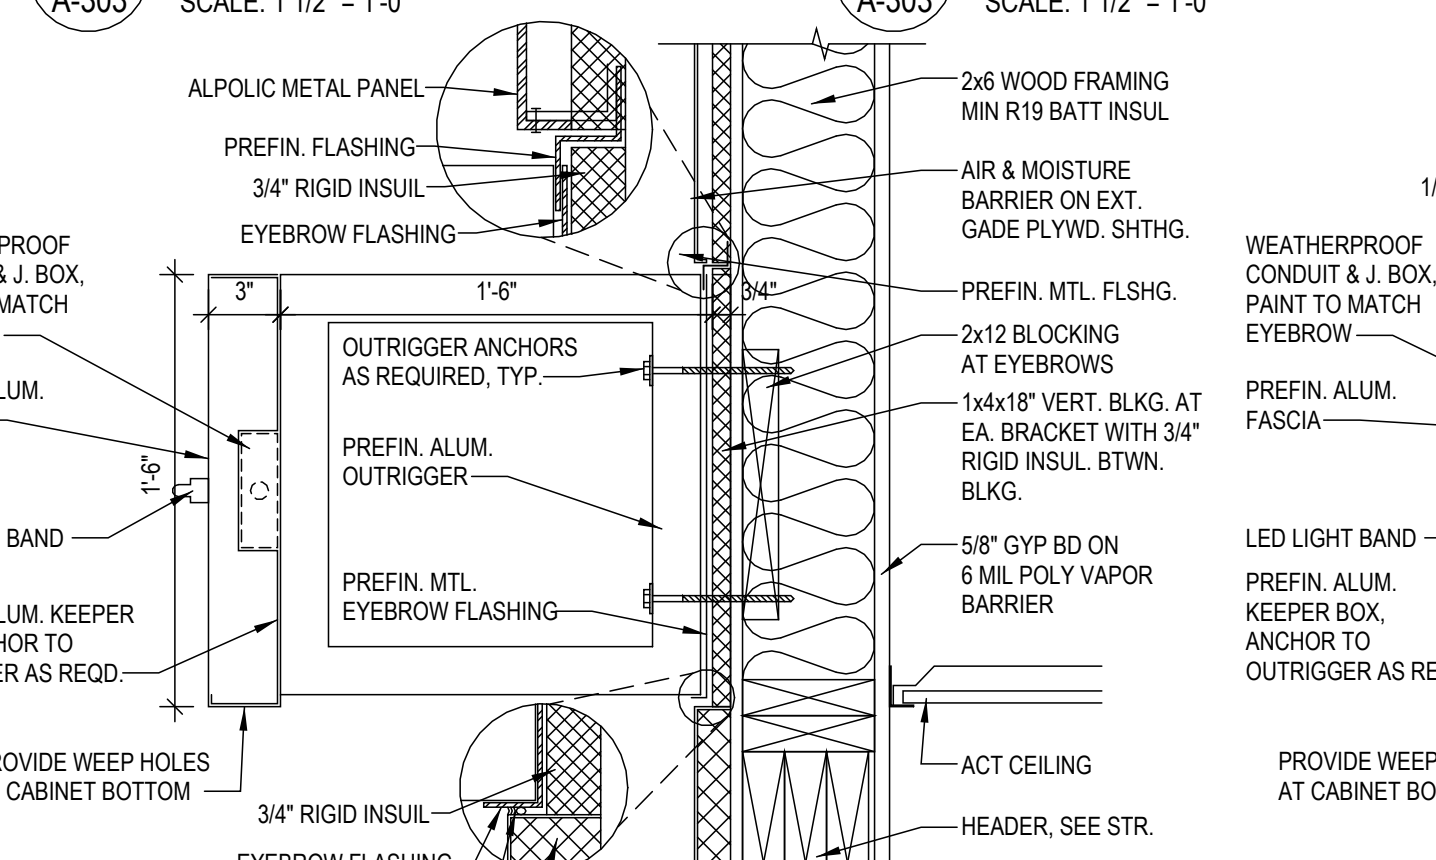


EYEBROW DETAIL-ALPOLIC


13 EYEBROW DETAIL-ALPOLIC
A-303 SCALE: 1 1/2" = 1'-0"

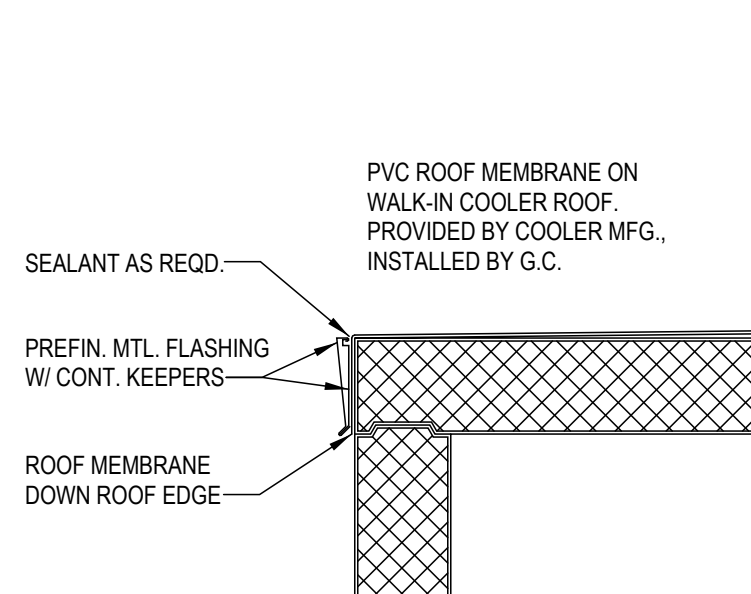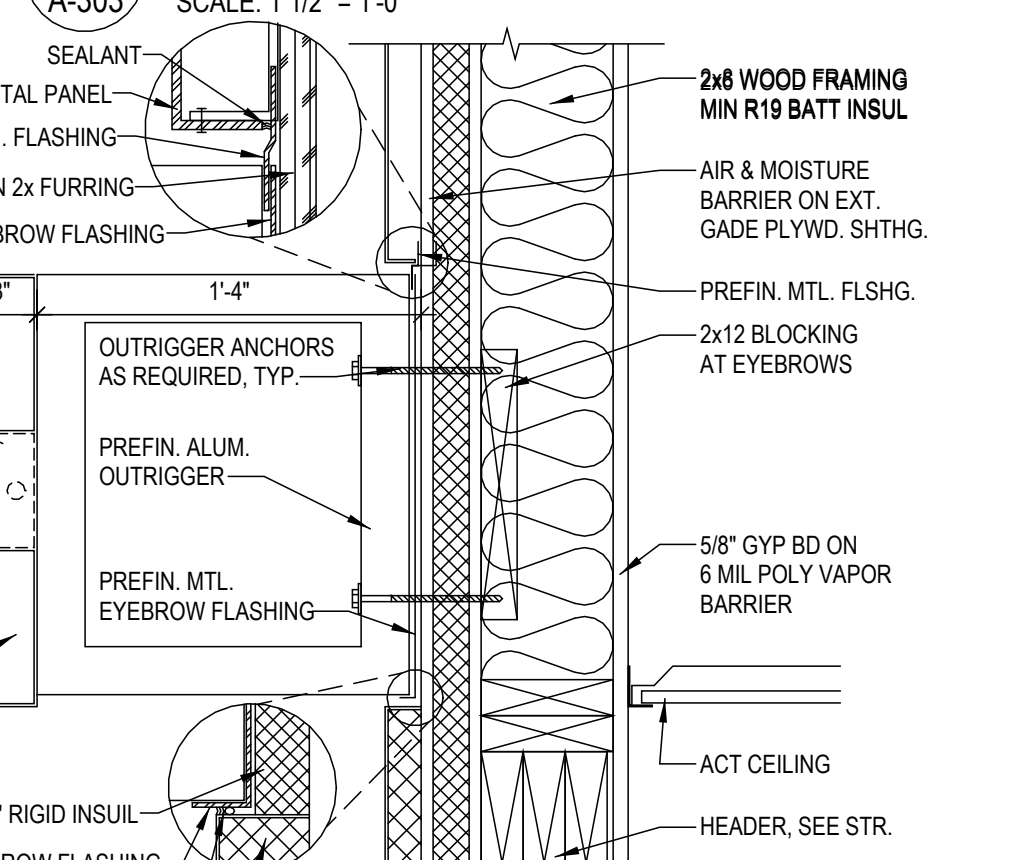


14 WALK-IN ROOF DETAIL
A-303 SCALE: 1 1/2" = 1'-0"

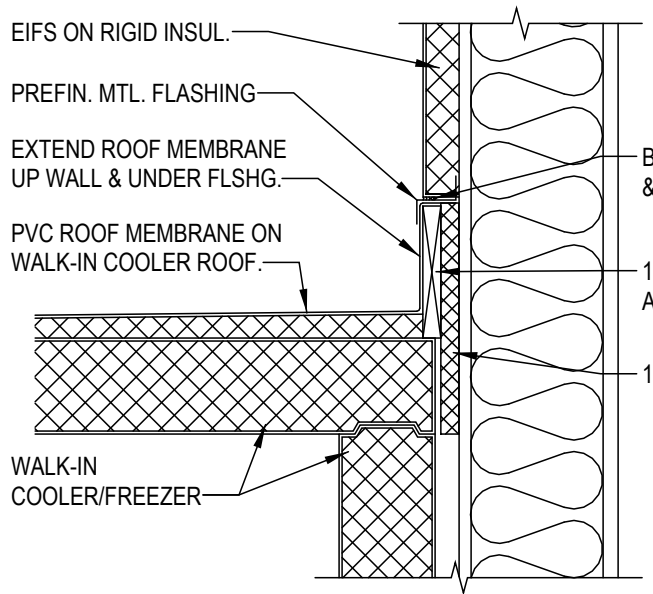


15 WALK-IN ROOF DETAIL
A-303 SCALE: 1 1/2" = 1'-0"

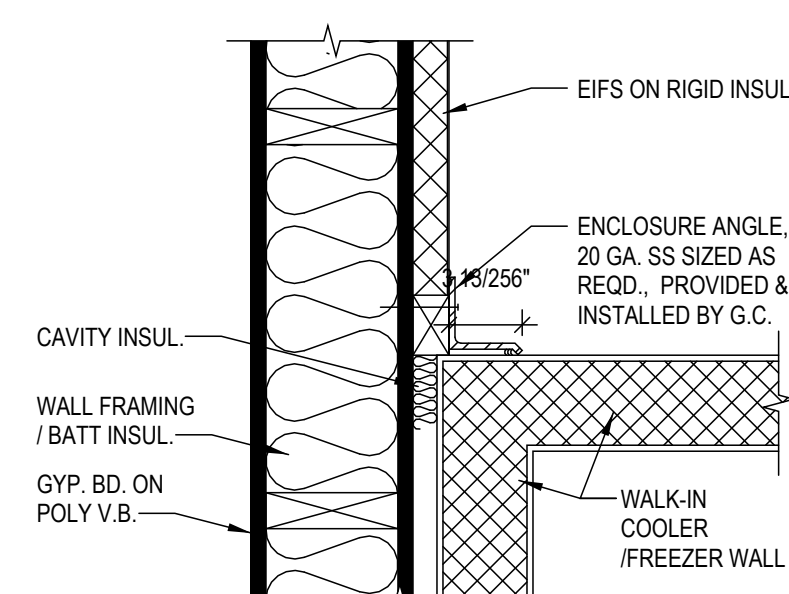


16 WALK-IN PLAN DETAIL
A-303 SCALE: 1 1/2" = 1'-0"

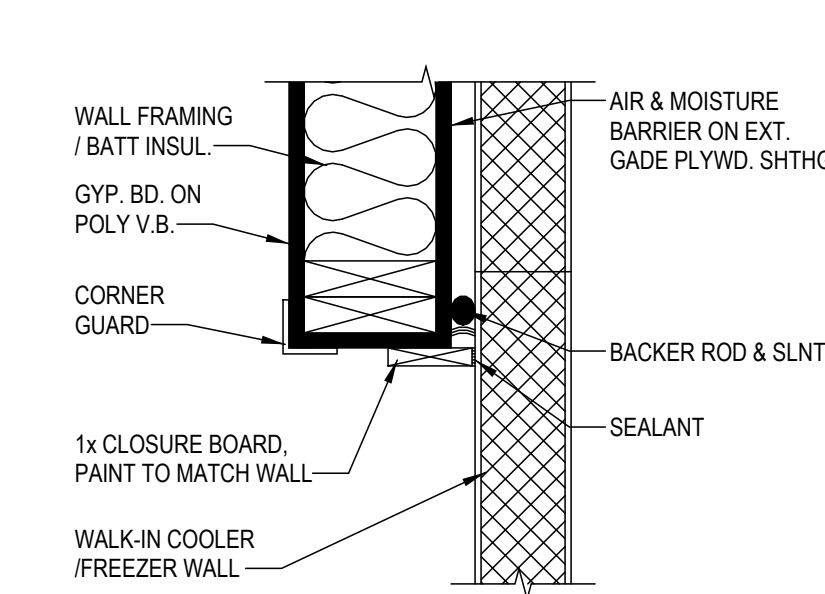


17 WALK-IN PLAN DETAIL
A-303 SCALE: 1 1/2" = 1'-0"

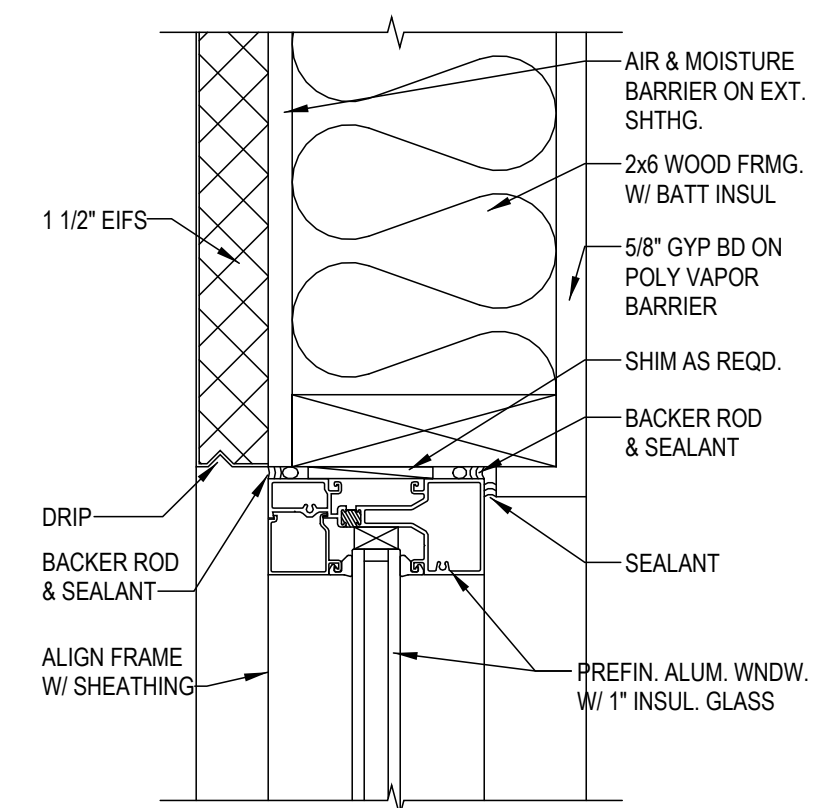

18 WINDOW HEAD DETAIL
A-303 SCALE: 3" = 1'-0"

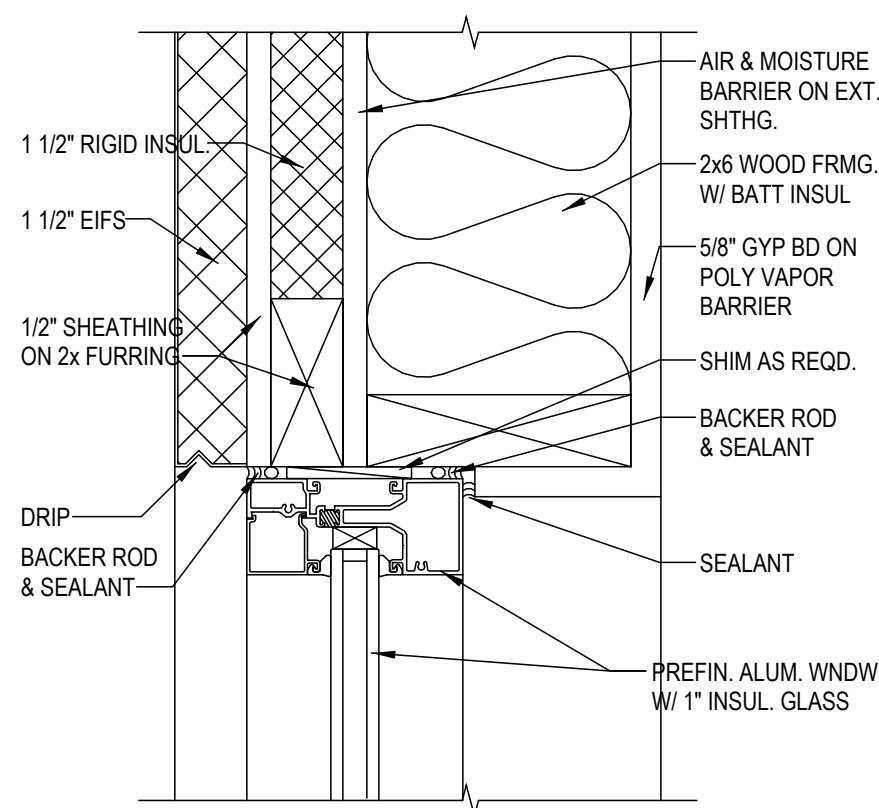

20 WINDOW HEAD DETAIL
A-303 SCALE: 3" = 1'-0"

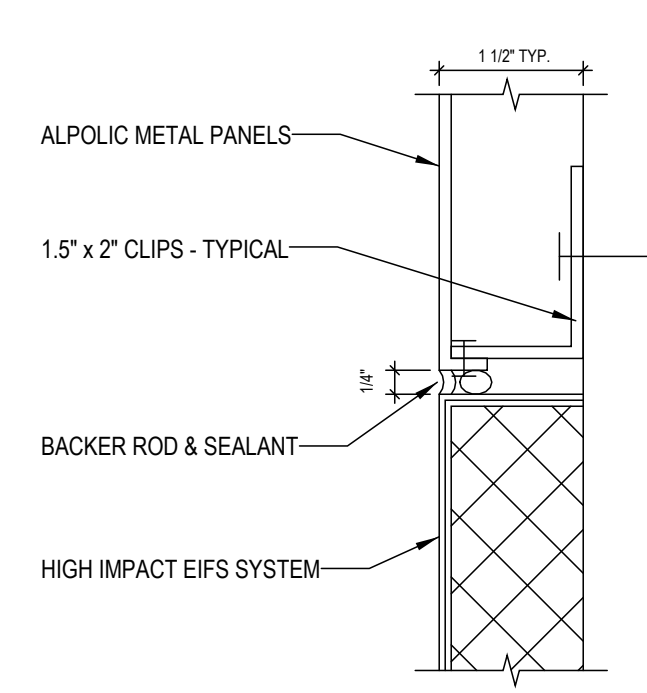

21 ALPOLIC/EIFS TRANSITION



REVISIONS:	
DELTA	DESCRIPTION
DATE	
DATE OF ISSUE:	04.13.2022
ISSUE PROJECT NO:	0559-2
PROJECT PHASE:	CD
DRAWN BY:	R