



4/14/2026 2:59:57 PM MERIDIAN ARCHITECTURE 0559-25 / DAIRY QUEEN - MANCHESTER - JAE DAMRON / SCHEMATIC DESIGN / A-304- WALL SECTIONS & DETAILS

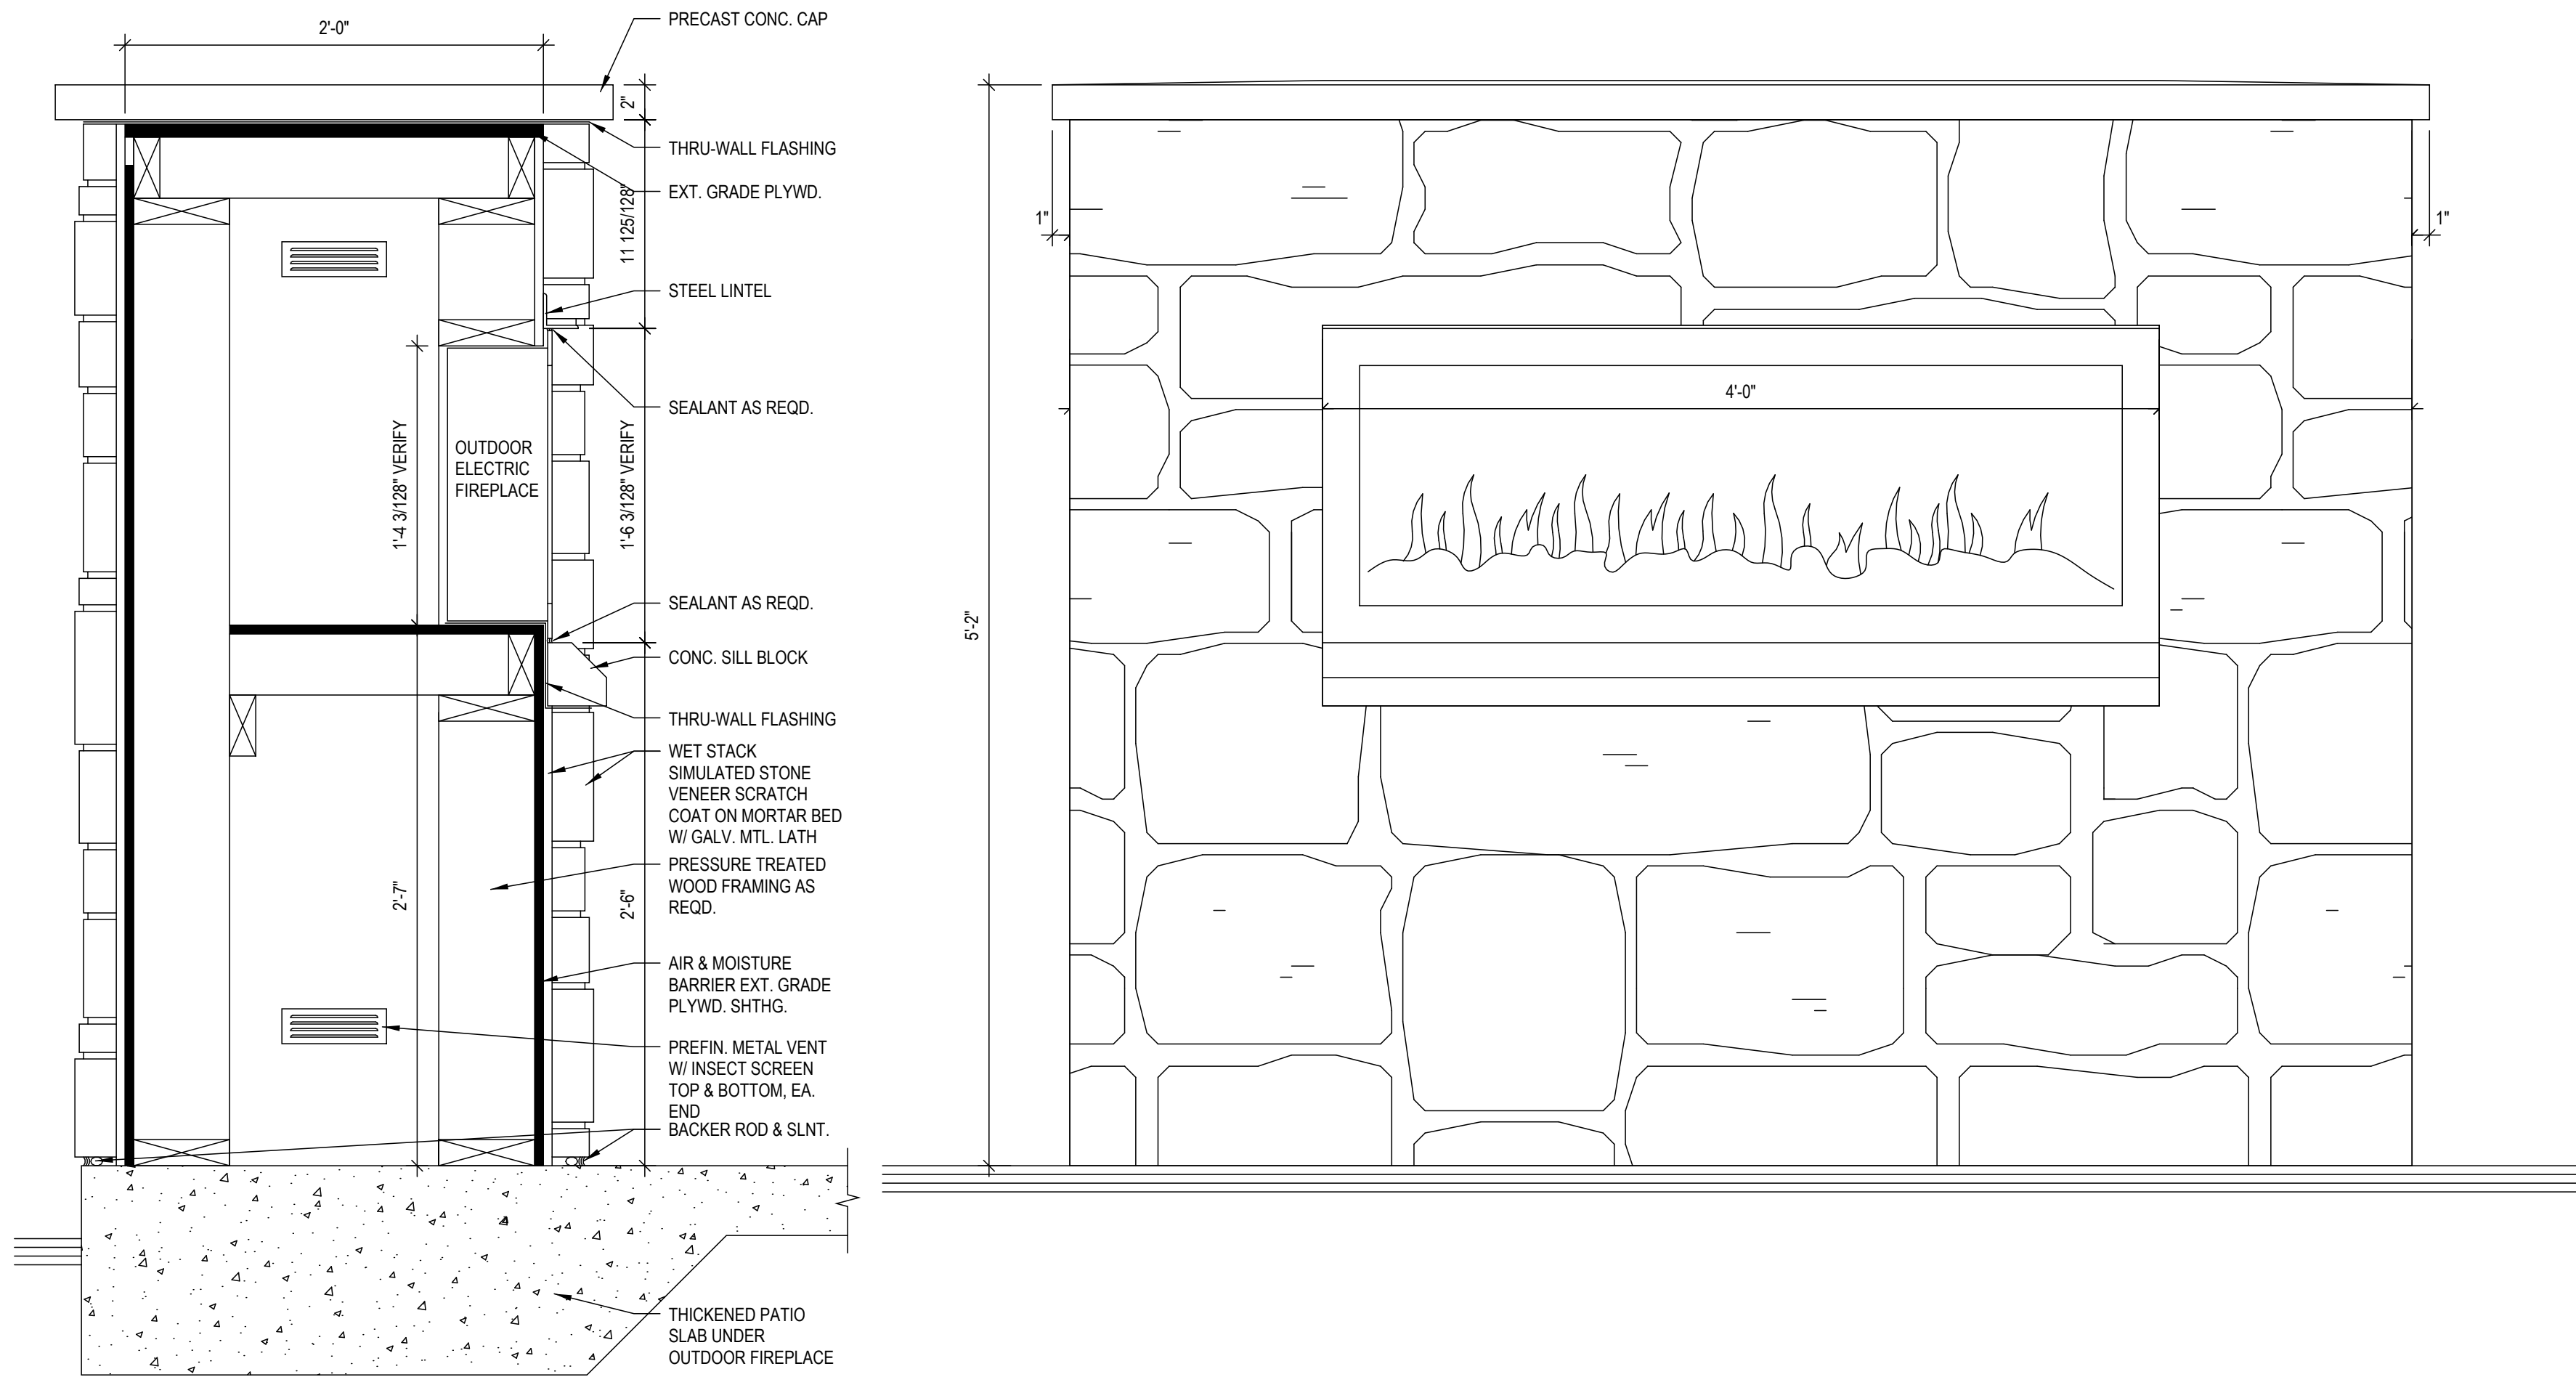

1 OPTIONAL OUTDOOR FIREPLACE DTL.
A4.4 SCALE: 1 1/2" = 1'-0"

2 OPTIONAL OUTDOOR FIREPLACE ELEVATION
A4.4 SCALE: 1 1/2" = 1'-0"

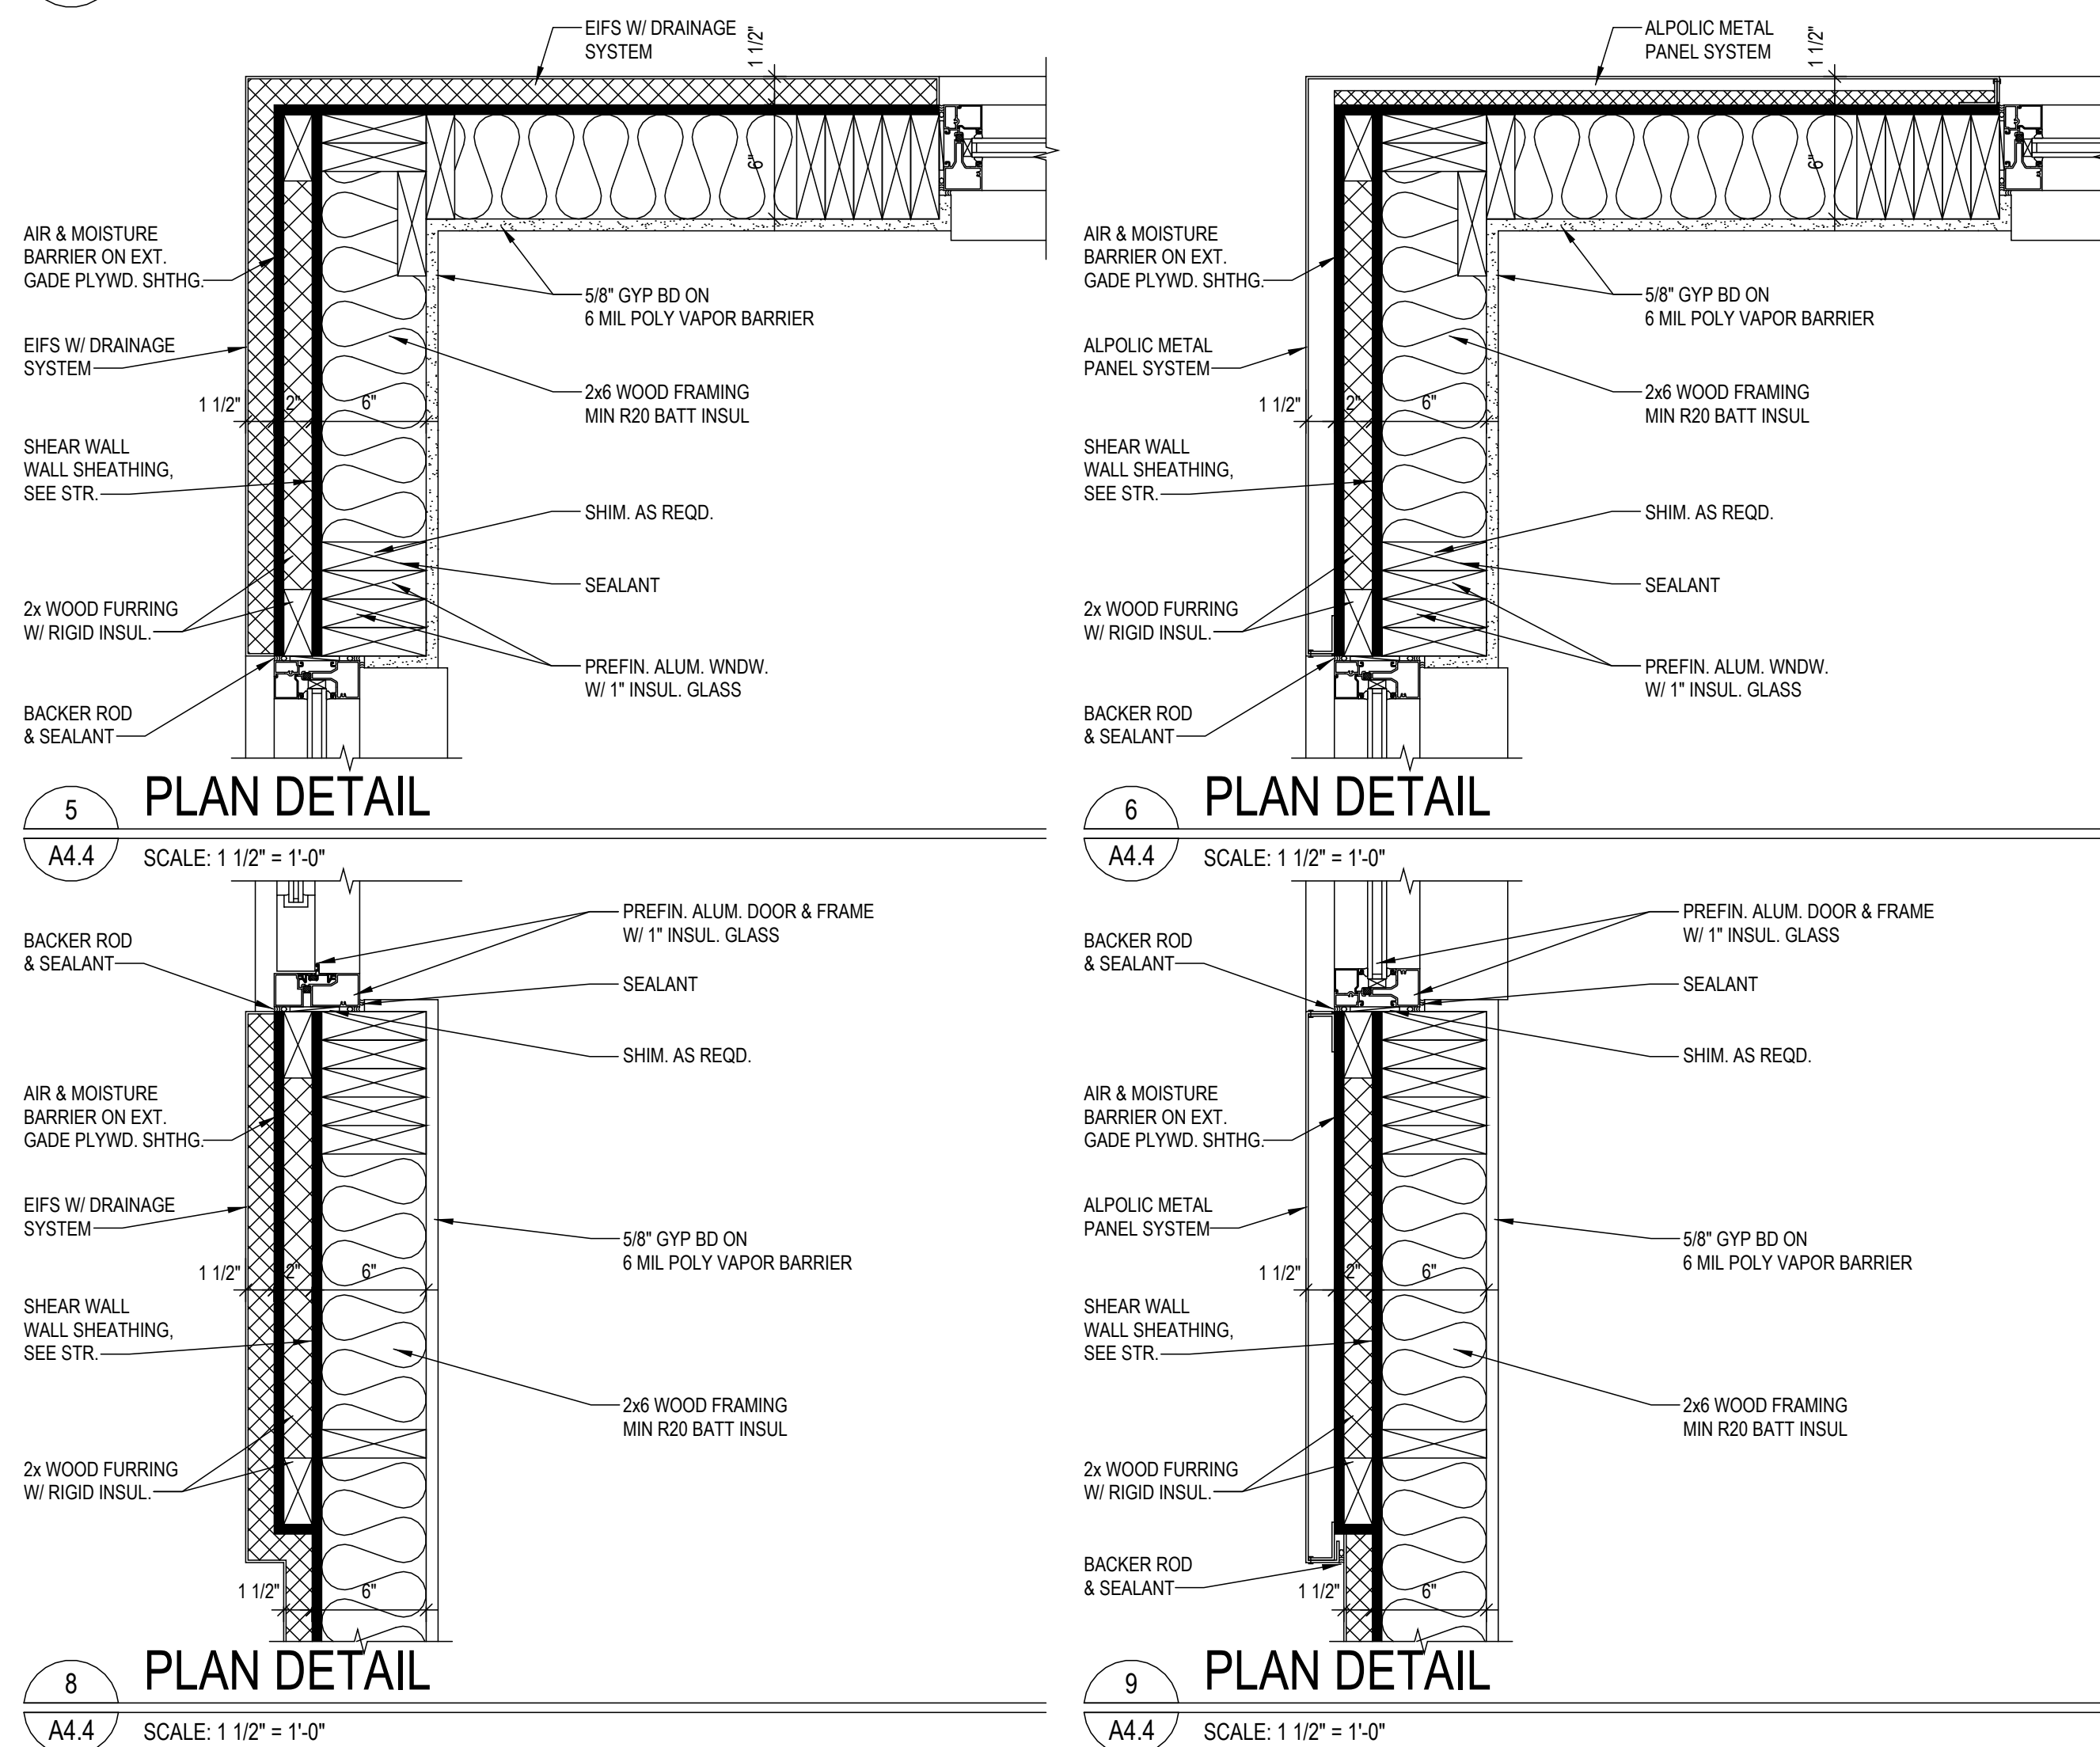

5 PLAN DETAIL
A4.4 SCALE: 1 1/2" = 1'-0"


6 PLAN DETAIL
A4.4 SCALE: 1 1/2" = 1'-0"

8 PLAN DETAIL
A4.4 SCALE: 1 1/2" = 1'-0"

9 PLAN DETAIL
A4.4 SCALE: 1 1/2" = 1'-0"

BUILDING SECTION GENERAL NOTES

- Suspended materials shall be attached to structure with tested connectors for tension or shear condition at frequency to support load applied.
- Insulation shall be continuous at the roof plane and shall lap wall insulation.
- Route all plumbing, fire sprinkler, mechanical, electrical, fire alarm, piping, and conduit in concealed or furred area only. Exposed piping and conduit shall not be allowed in any area except at electrical and fire riser rooms.

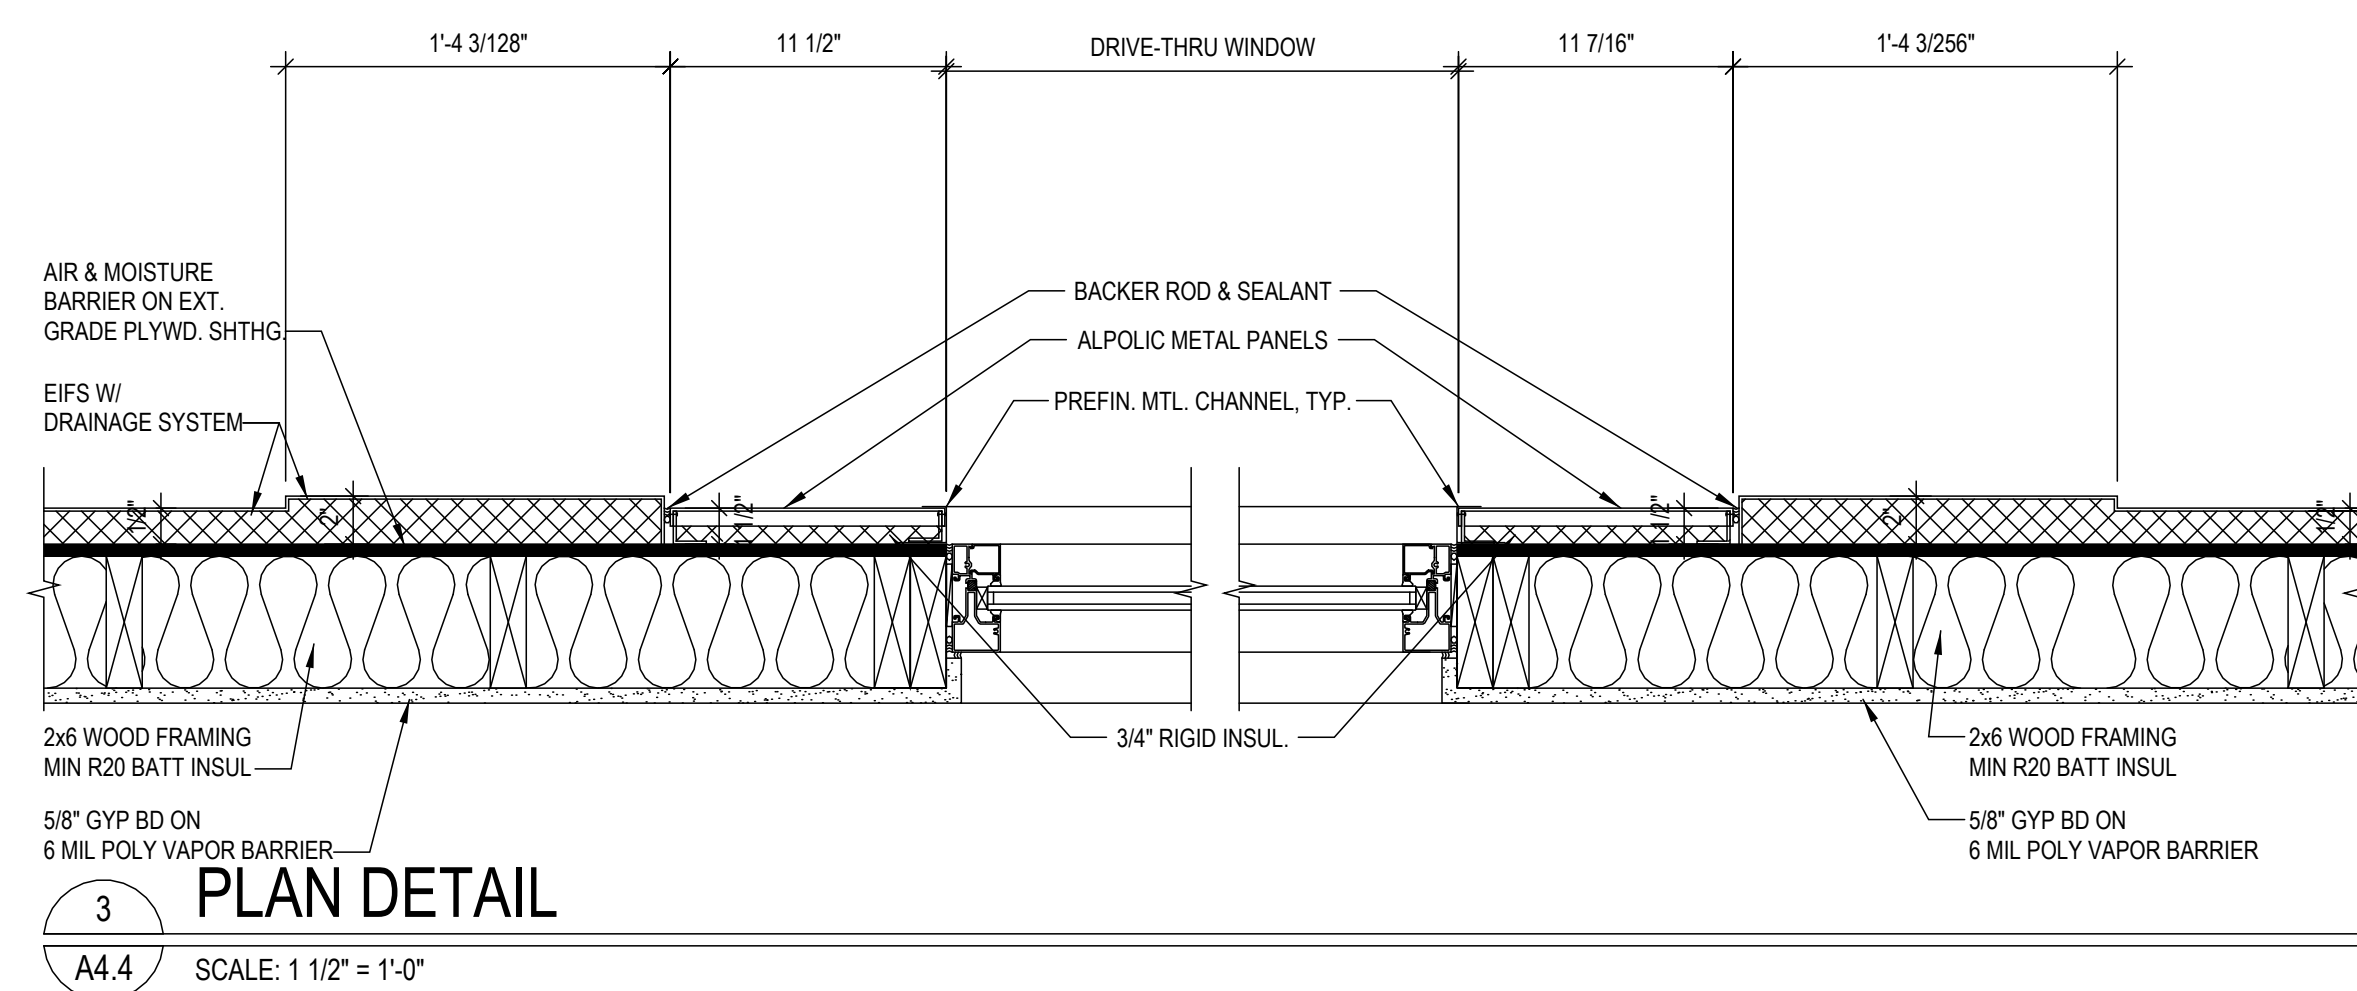

3 PLAN DETAIL
A4.4 SCALE: 1 1/2" = 1'-0"

DAIRY QUEEN - MANCHESTER

JAE DAMRON
Manchester, TN

CLIENT CONTACT:
JAE DAMRON | HIGHWAY 53 | MANCHESTER, TN 37349
(931) 273-7166 | jae@jadedamronventures.com

MERIDIAN ARCHITECTURE



nashville, tennessee
e: office@meridiamn.com
t: 615.350.2236
www.meridiamn.com

REVISIONS:

DELTA	DESCRIPTION	DATE
-------	-------------	------

DATE OF ISSUE:	04.13.2026
----------------	------------

MA PROJECT NO:	0559-25
----------------	---------

PROJECT PHASE:	CD
----------------	----

DRAWN BY:	RP
-----------	----

WALL SECTIONS &
DETAILS

A-304