


DAIRY QUEEN - MANCHESTER

JAIE DAMRON
Manchester, TN

CLIENT CONTACT:
JAE DAMRON | HIGHWAY 53 | MANCHESTER, TN 37349
(931) 273-7166 | jae@damronventures.com

MERIDIAN | ARCHITECTURE

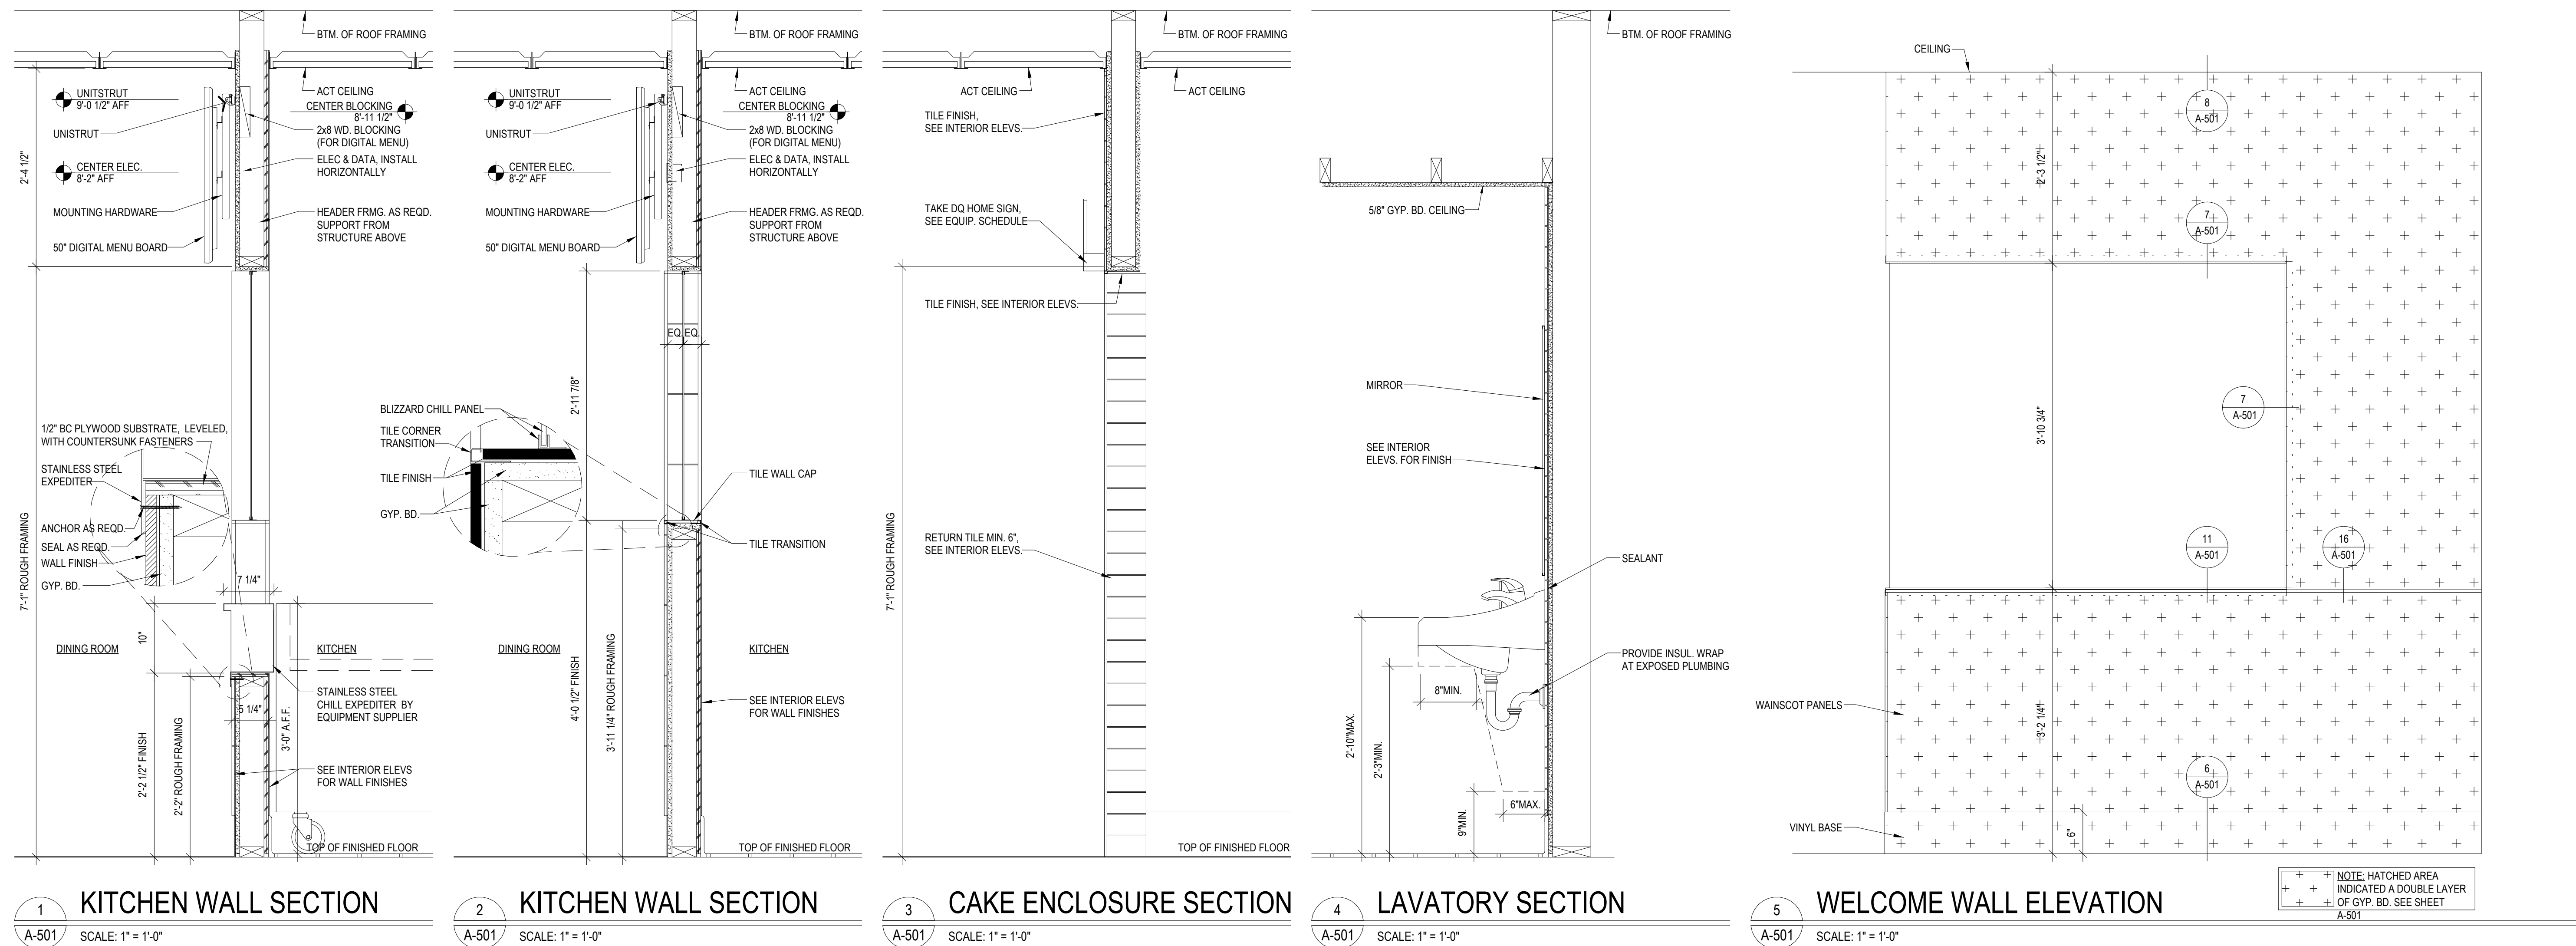

nashville, tennessee
e: office@meridiantn.com
t: 615.390.2236
www.meridiantn.com

REVISIONS:		
DELTA	DESCRIPTION	DATE
DATE OF ISSUE:		04.13.2025
MA PROJECT NO:		0559-2
PROJECT PHASE:		CR
DRAWN BY:		R

DETAILS

A-501