




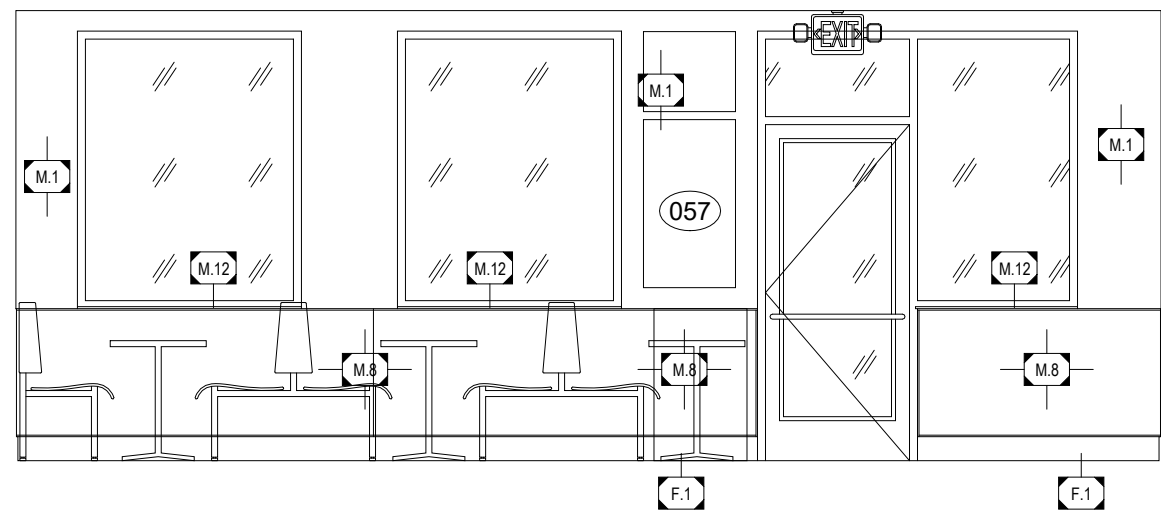


1 INTERIOR ELEVATION
Scale is 1/4" = 1'-0" when printed full size.

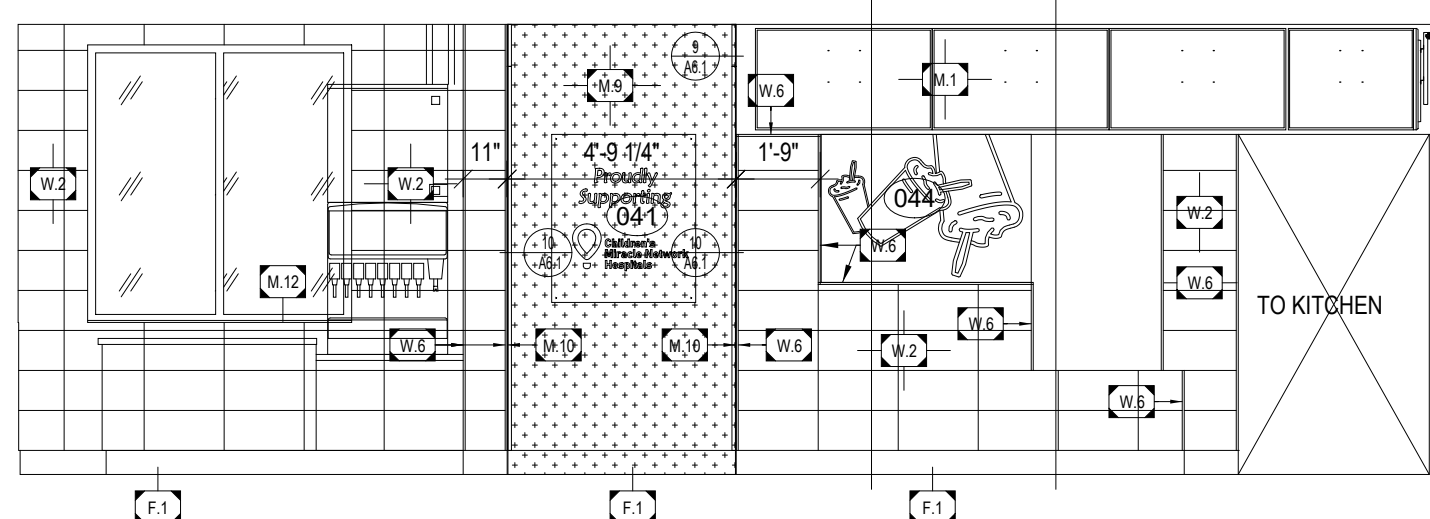


2 INTERIOR ELEVATION
Scale is 1/4" = 1'-0" when printed full size.

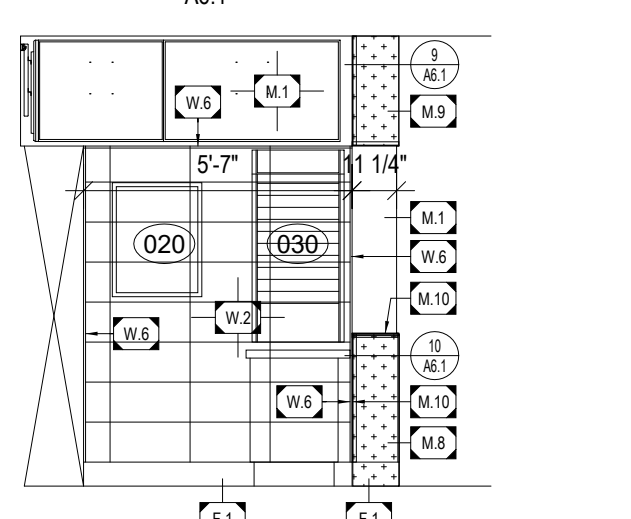


3 INTERIOR ELEVATION
Scale is 1/4" = 1'-0" when printed full size.

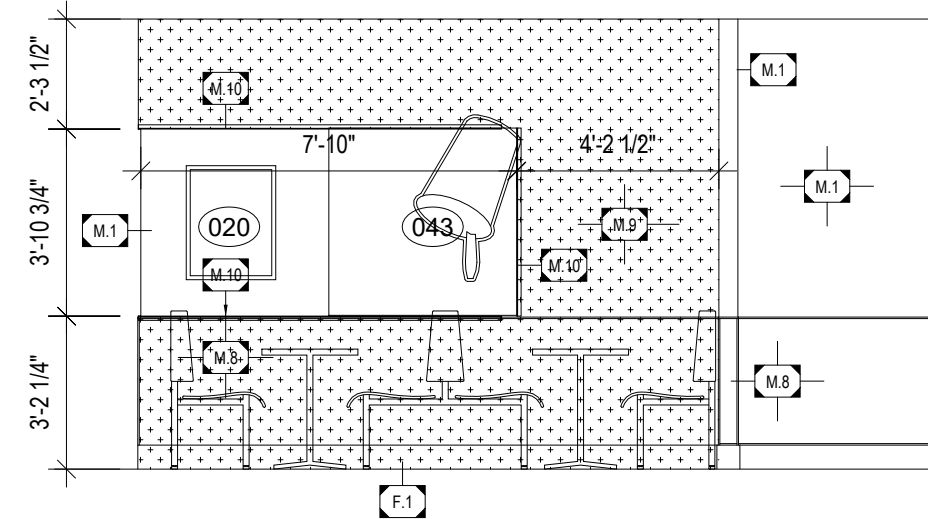


4 INTERIOR ELEVATION
Scale is 1/4" = 1'-0" when printed full size.

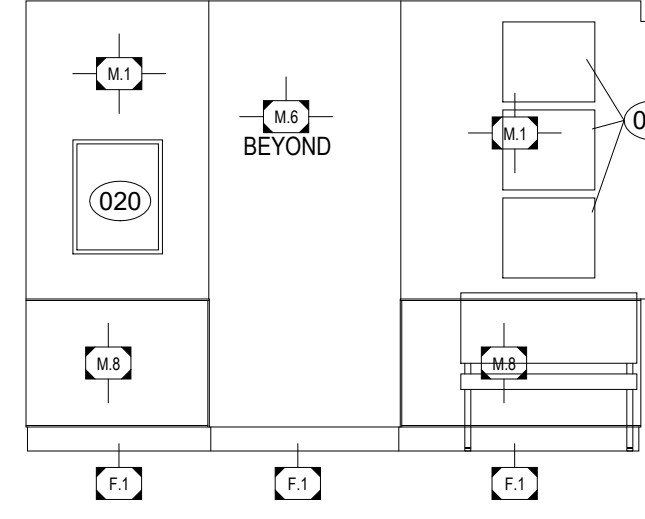


5 INTERIOR ELEVATION
Scale is 1/4" = 1'-0" when printed full size.

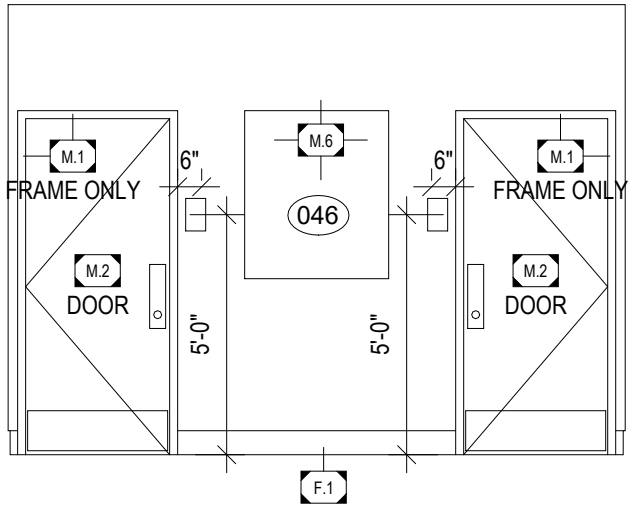


6 INTERIOR ELEVATION
Scale is 1/4" = 1'-0" when printed full size.

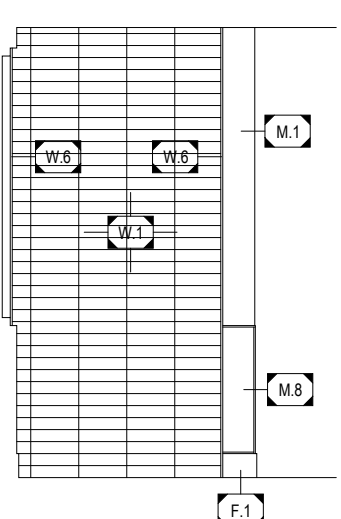


7 INTERIOR ELEVATION
Scale is 1/4" = 1'-0" when printed full size.

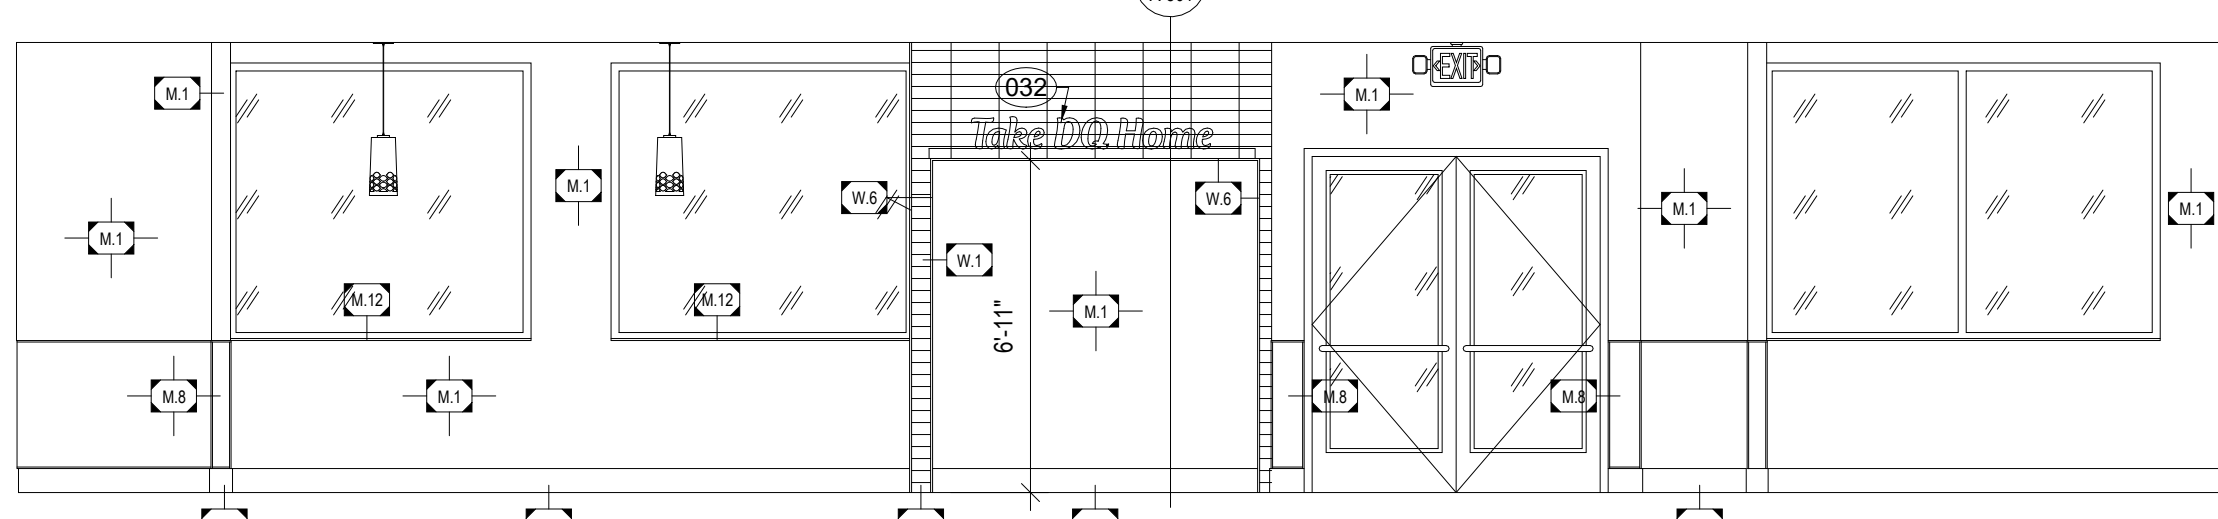


8 INTERIOR ELEVATION
Scale is 1/4" = 1'-0" when printed full size.

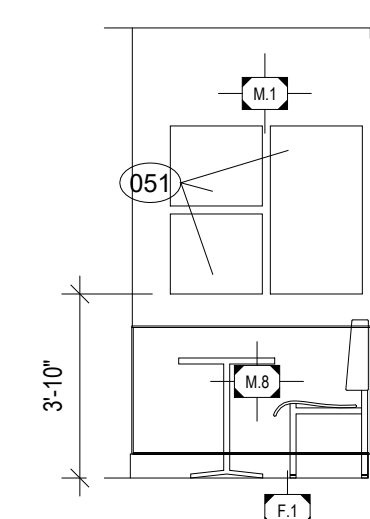


9 INTERIOR ELEVATION
Scale is 1/4" = 1'-0" when printed full size.

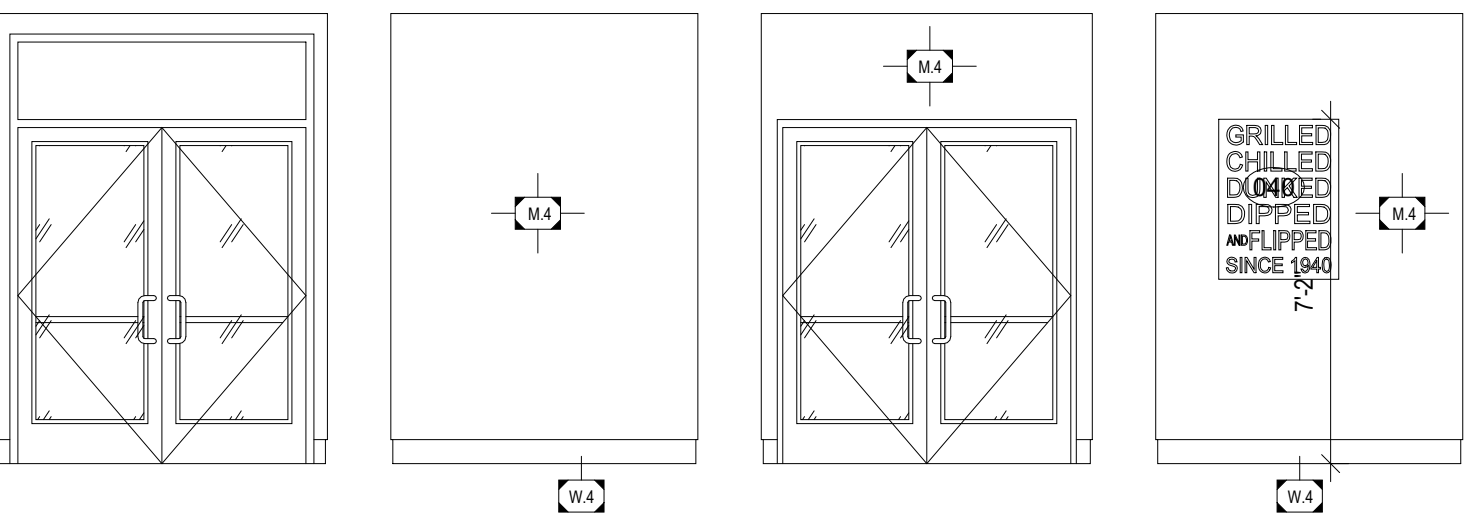


10 INTERIOR ELEVATION
Scale is 1/4" = 1'-0" when printed full size.

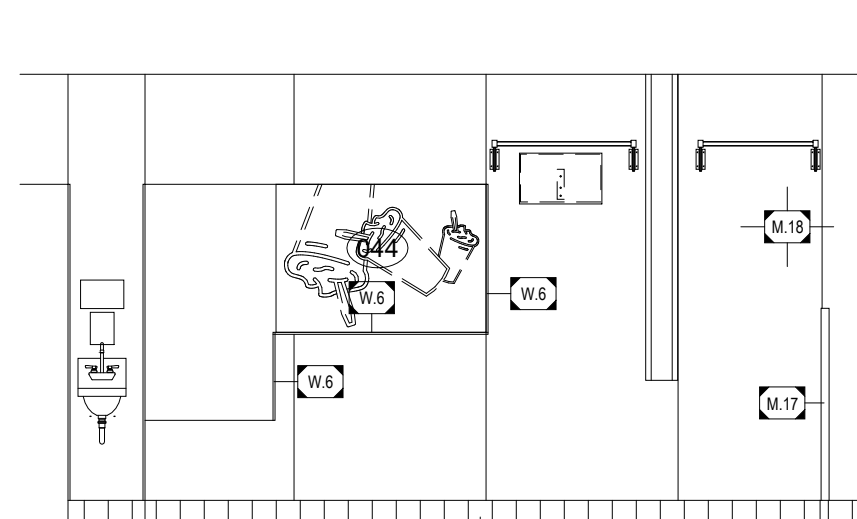


11 INTERIOR ELEVATION
Scale is 1/4" = 1'-0" when printed full size.

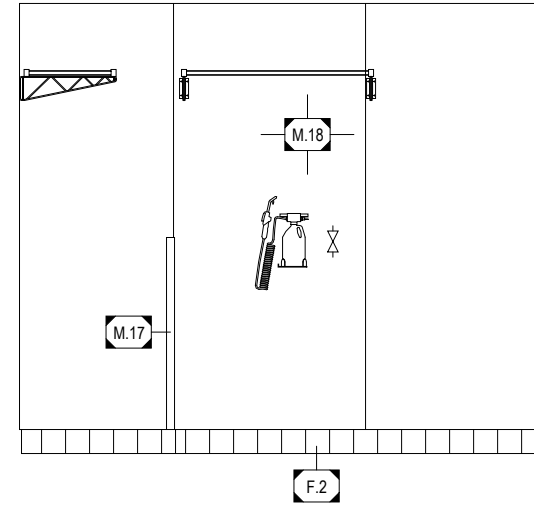


12 INTERIOR ELEVATION
Scale is 1/4" = 1'-0" when printed full size.

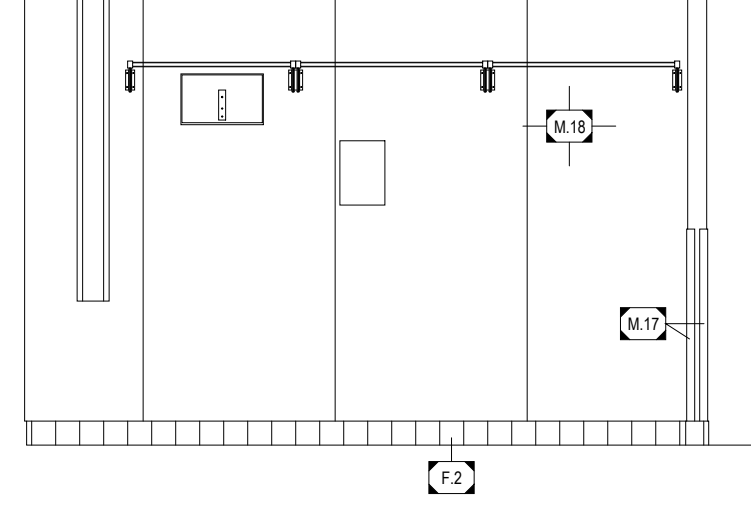


13 INTERIOR ELEVATION
Scale is 1/4" = 1'-0" when printed full size.

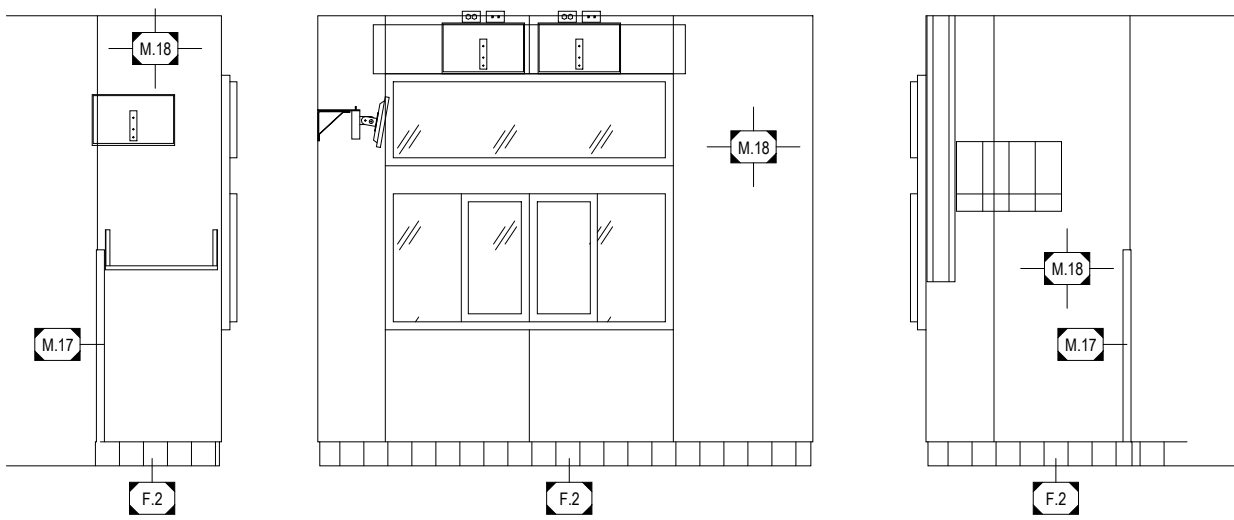


14 INTERIOR ELEVATION
Scale is 1/4" = 1'-0" when printed full size.

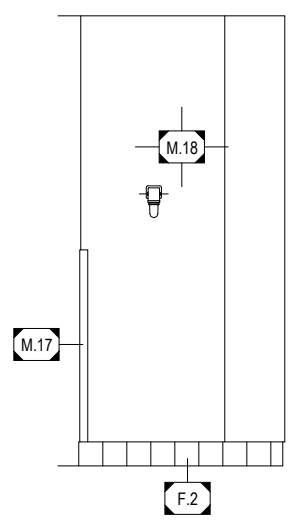


15 INTERIOR ELEVATION
Scale is 1/4" = 1'-0" when printed full size.

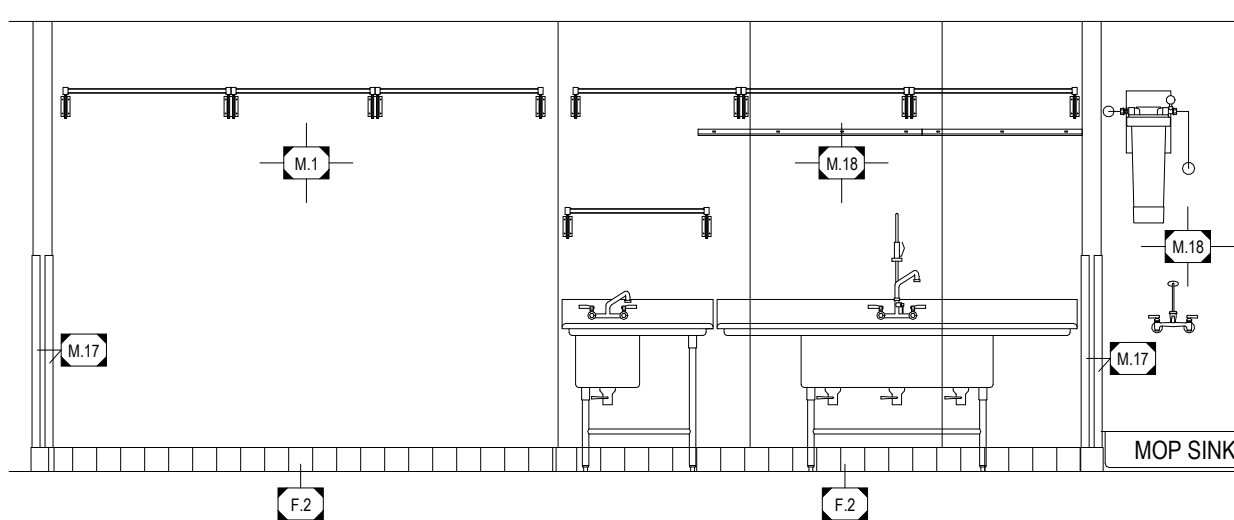


16 INTERIOR ELEVATION
Scale is 1/4" = 1'-0" when printed full size.

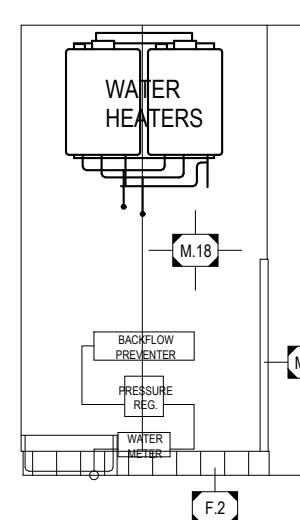


17 INTERIOR ELEVATION
Scale is 1/4" = 1'-0" when printed full size.

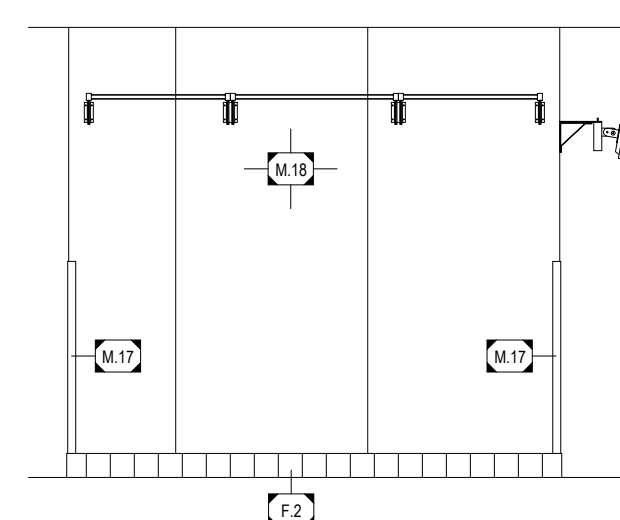


18 INTERIOR ELEVATION
Scale is 1/4" = 1'-0" when printed full size.

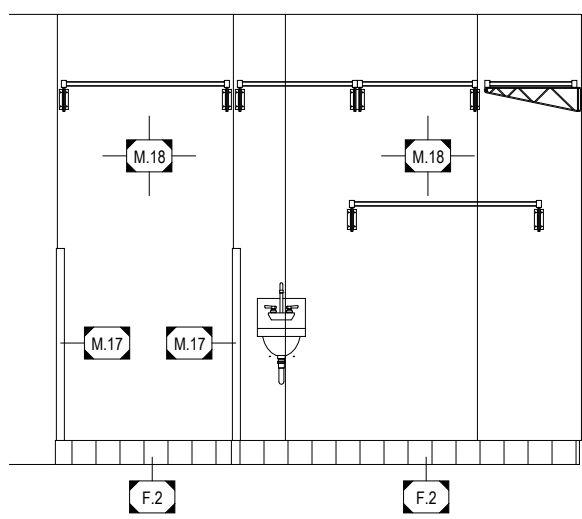


19 INTERIOR ELEVATION
Scale is 1/4" = 1'-0" when printed full size.

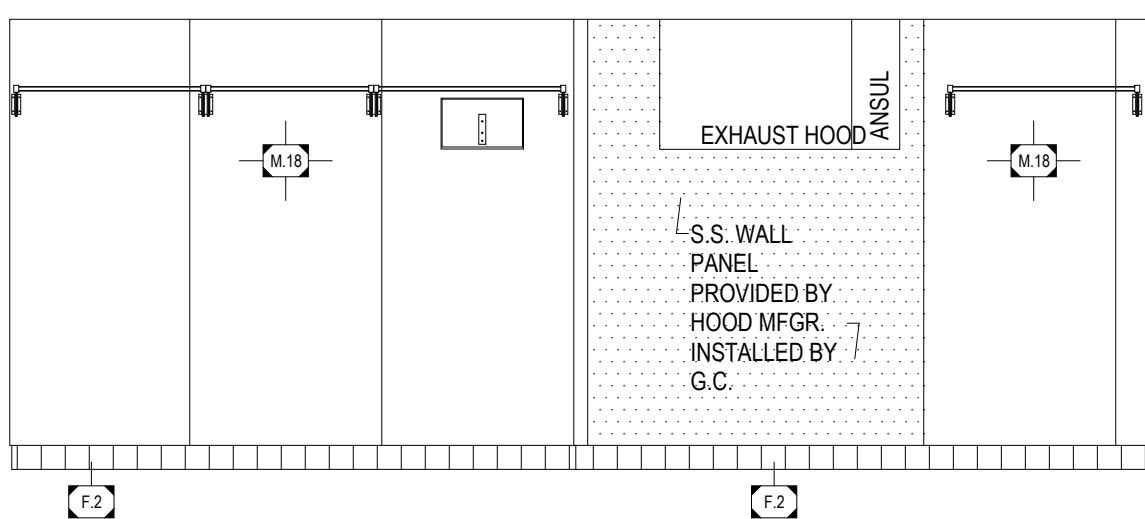


20 INTERIOR ELEVATION
Scale is 1/4" = 1'-0" when printed full size.

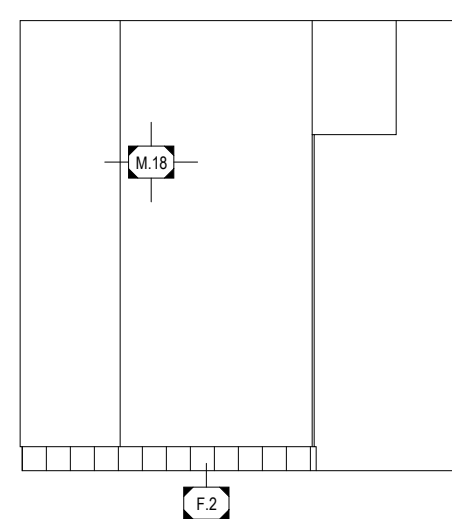


21 INTERIOR ELEVATION
Scale is 1/4" = 1'-0" when printed full size.

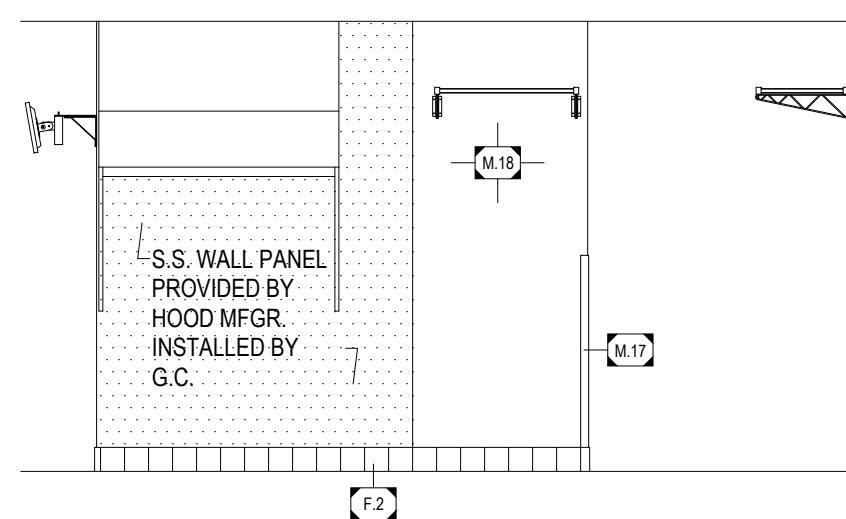

22 INTERIOR ELEVATION
Scale is 1/4" = 1'-0" when printed full size.

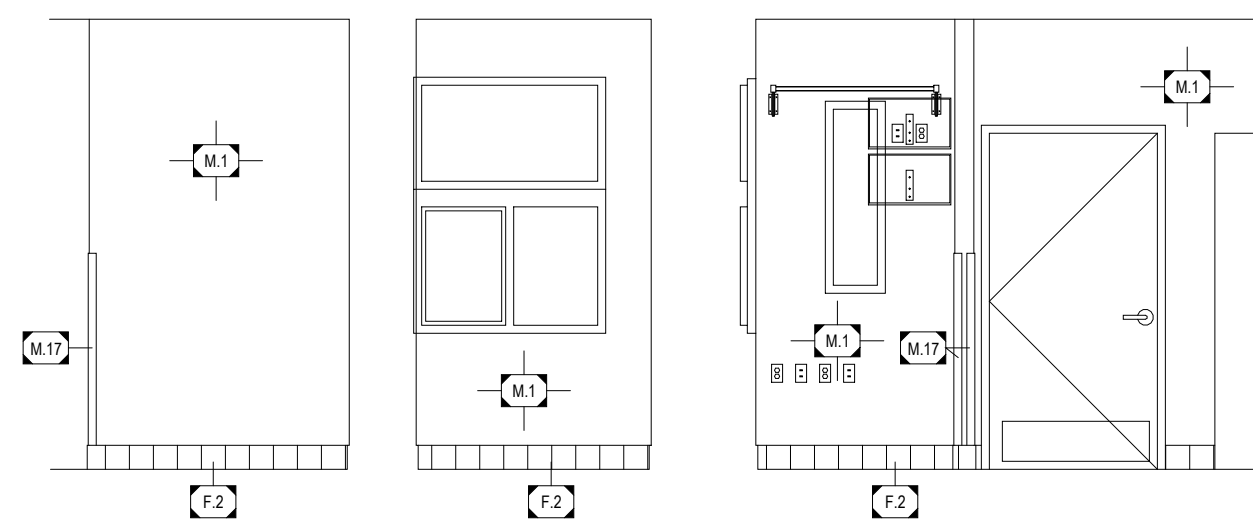

23 INTERIOR ELEVATION
Scale is 1/4" = 1'-0" when printed full size.

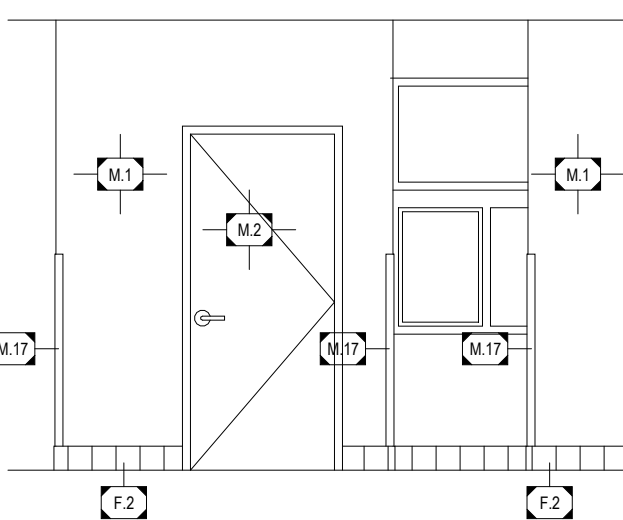

24 INTERIOR ELEVATION
Scale is 1/4" = 1'-0" when printed full size.

