

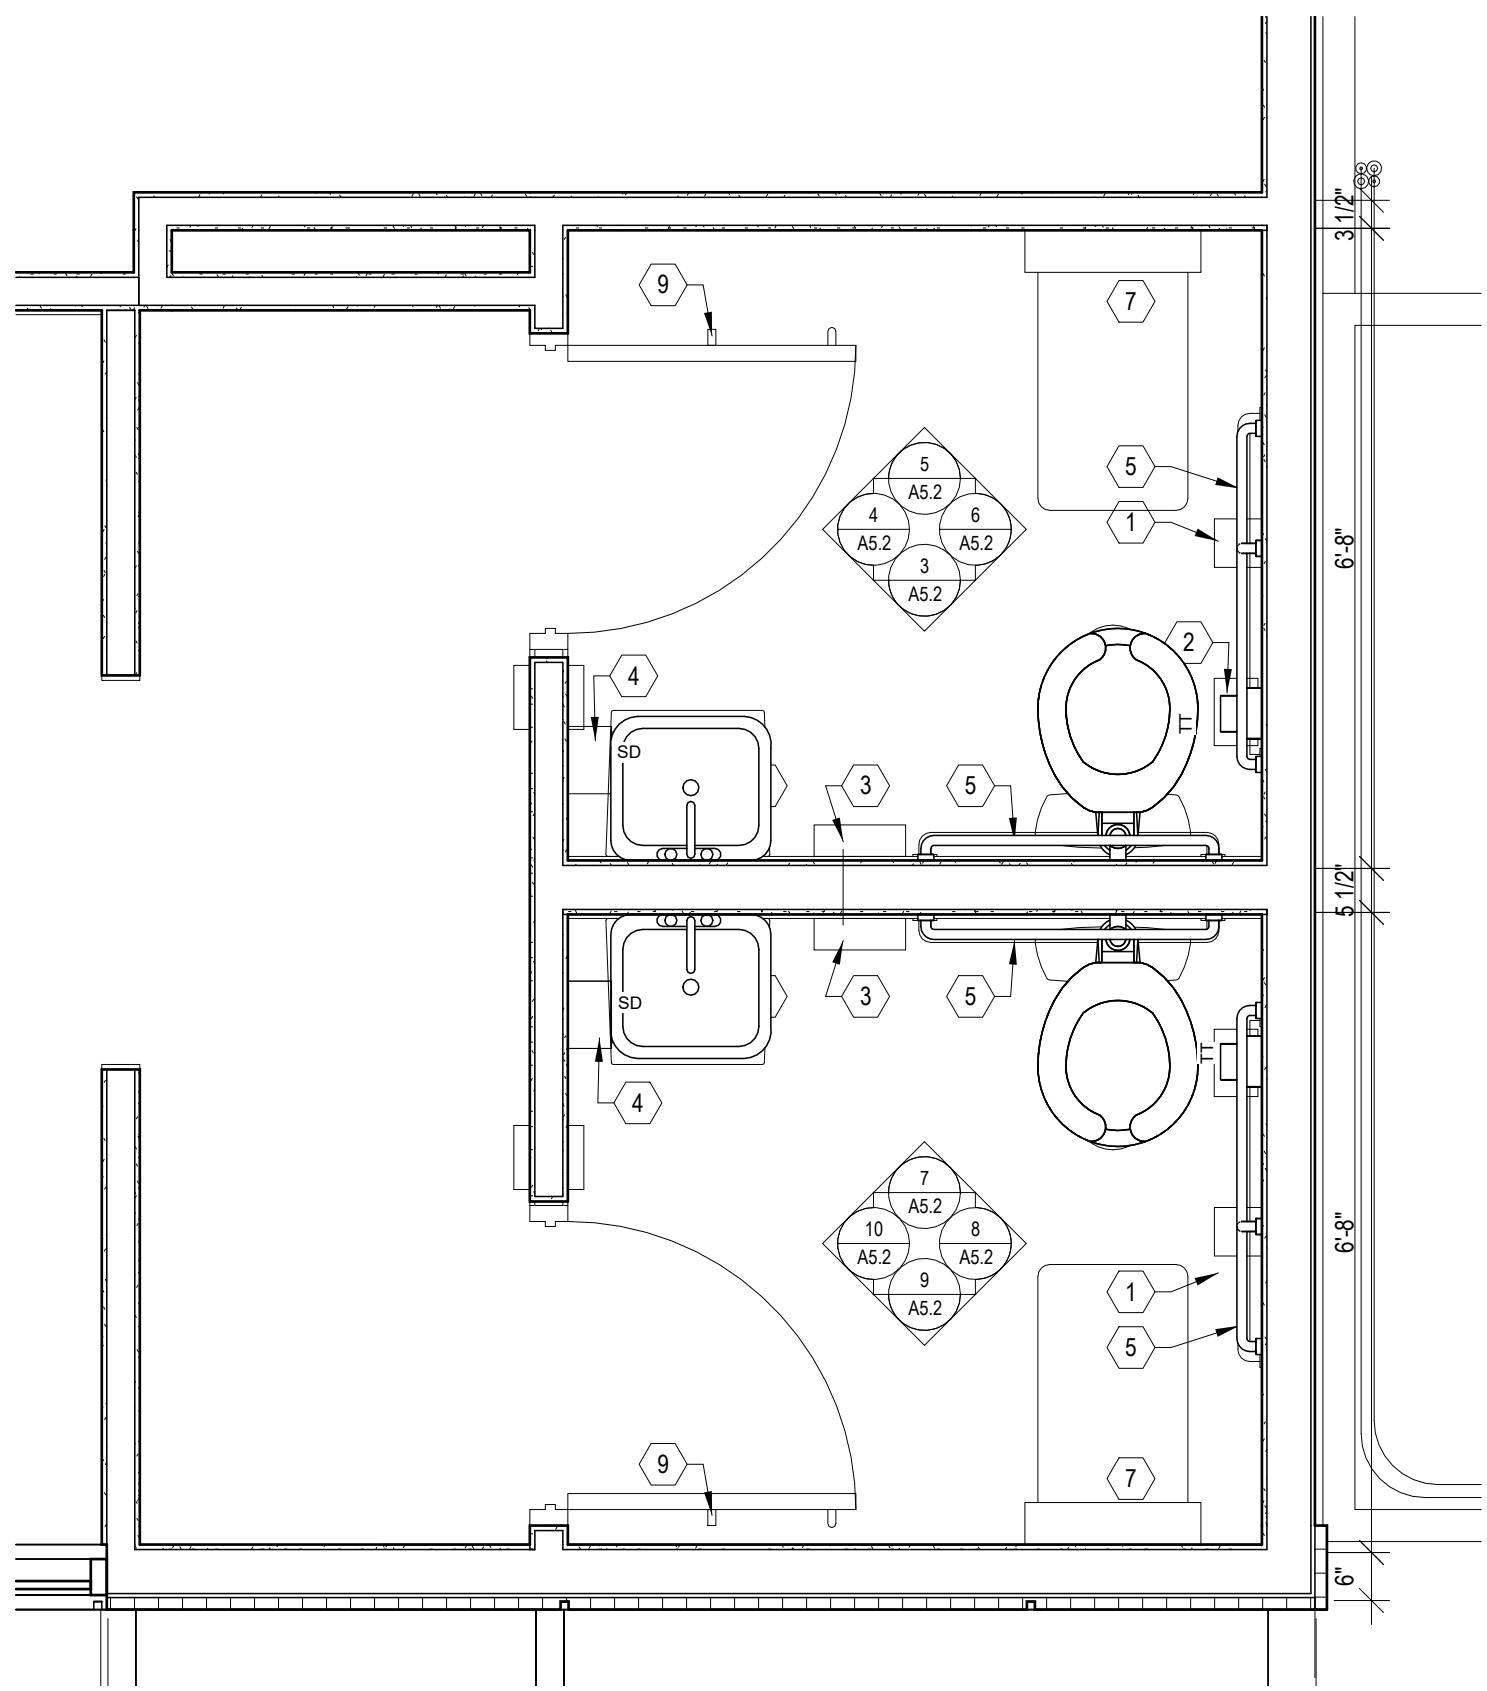


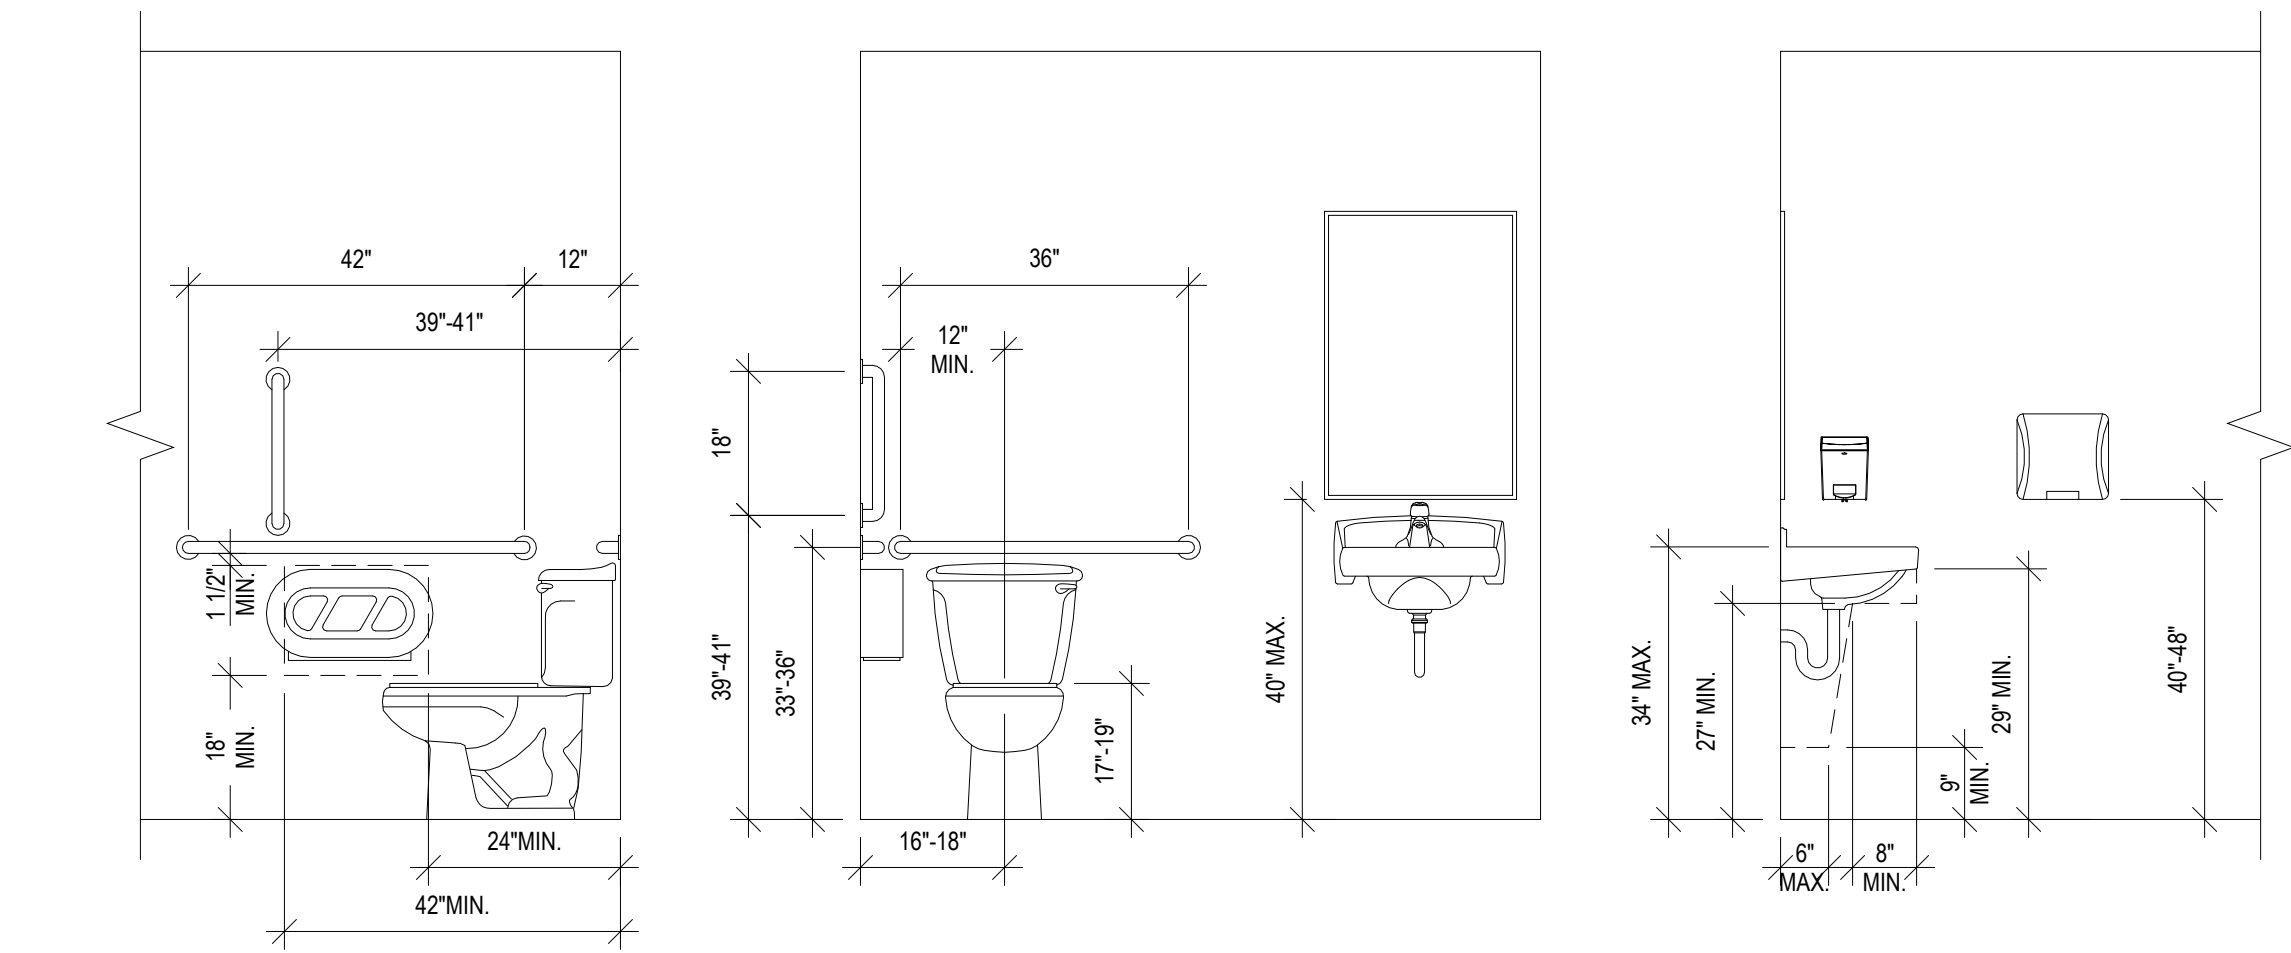

RESTROOM FLOOR PLAN

0 20' 40' 60'
1/2" = 1'-0"

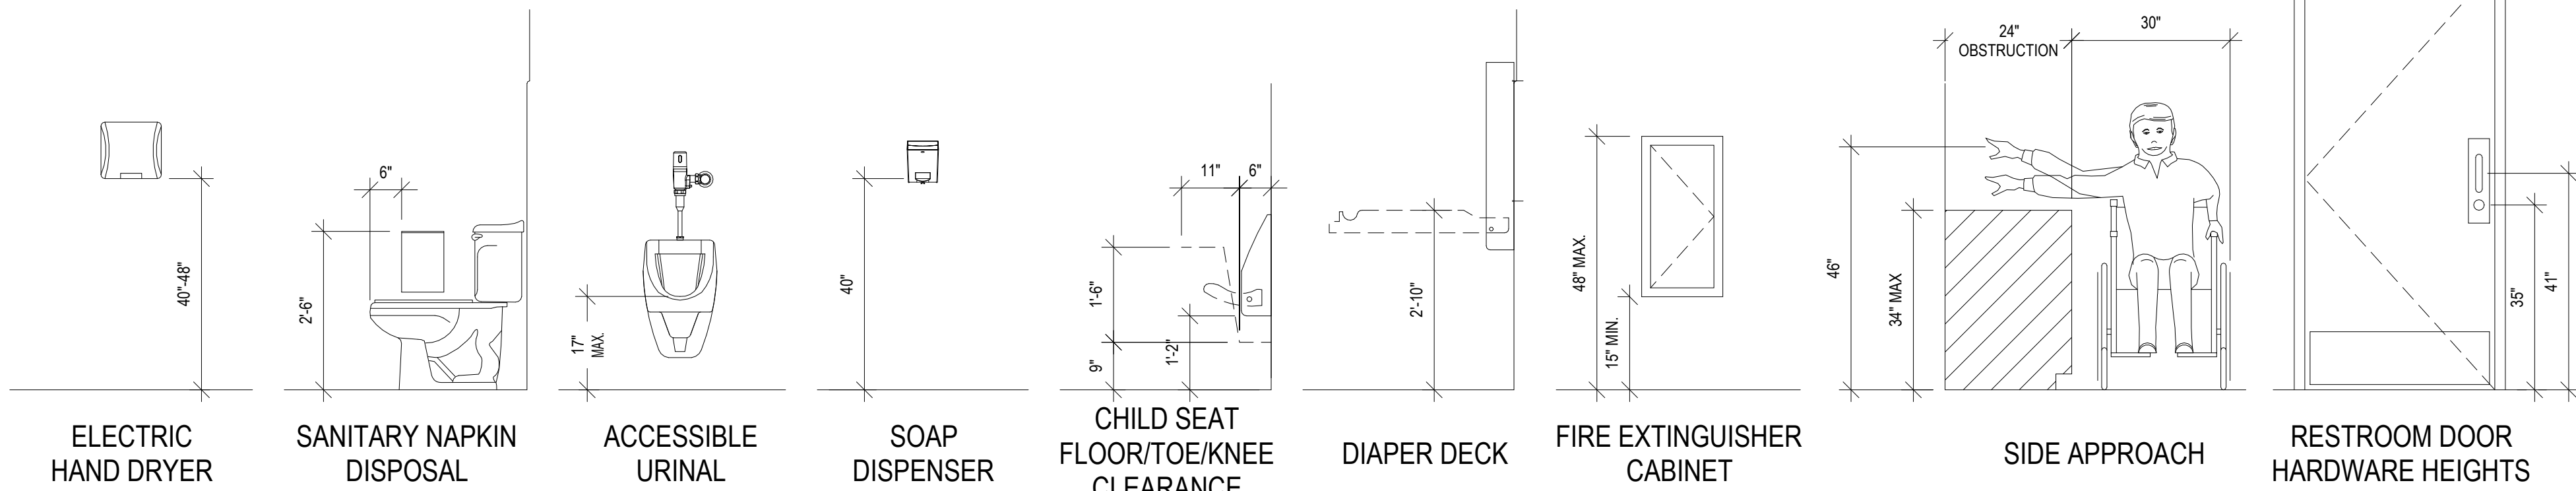

2 ADA Mounting Heights

1/2" = 1'-0"
0 2' 4' 6'

TOILET ACCESSORY SCHEDULE:			
1	TOILET PAPER DISPENSER	[C] [D]	
2	SANITARY NAPKIN RECEPTICAL	BOBRICK [A] [B]	B-270
3	ELECTRIC HAND DRYER	WORLD [B]	SLIM6H L-973
4	AUTOMATIC SOAP DISPENSER	[C]	
5	GRAB BARS	BOBRICK [A] [B]	B-6806
6	GRAB BAR ANCHORS	BOBRICK [A] [B]	252-30
7	DIAPER DECK (MOUNT DECK AT 34" A.F.F.)	FOUNDATIONS [A] [B]	100-EV, LIGHT GRAY
8	CHILD SEAT (MOUNT BTM AT 14" A.F.F.)	FOUNDATIONS [A] [B]	103-BQS, LIGHT GRAY
9	COAT HOOK (MOUNT AT 4'-0" A.F.F.)	BRADLEY [A] [B]	9134
10	WALL MIRROR (24"x36")	MEEK MIRROR [A] [B]	IM1510
11	ADA UNDERSINK DRAIN AND SUPPLY COVERS	MAINLINE [A] [B]	ML102EZ
12	AUTOMATIC PAPER TOWEL DISPENSER	[C] [D]	

[A] RECOMMENDED MANUFACTURER & MODEL
[B] PROVIDED AND INSTALLED BY G.C. AVAILABLE FROM HUC
[C] DISPENSERS ARE AVAILABLE AS PART OF VENDORS OPENING PACKAGE, COORDINATE WITH FRANCHISEE & VENDOR. INSTALLED BY G.C.
[D] ALTERNATE DISPENSERS ARE AVAILABLE THROUGH HUC, PROVIDED & INSTALLED BY G.C.

GENERAL NOTES:
1. LAVATORY TO BE AUTOMATIC SENSOR CONTROLLED AND WATER CLOSETS TO BE LEVER TYPE CONTROL
2. GRAB BAR AND SEAT SHALL WITHSTAND A LOAD OF NOT LESS THAN 250 POUNDS APPLIED AT ANY POINT. PROVIDE BLOCKING AS REQUIRED.
3. PROVIDE 1 1/2" CLEARANCE BETWEEN GRAB BAR AND WALL
4. HOT WATER AND DRAIN PIPES UNDER LAVATORY SHALL BE INSULATED OR OTHERWISE CONFIGURED TO PROTECT AGAINST CONTACT.
5. PROVIDE SMOOTH, HARD, NON-ABSORBANT SURFACE ON FLOORS & WALLS WITHIN 24" OF URINAL AND WATERCLOSET & EXTENDING MIN. 48" UP
6. PROVIDE BLOCKING AS REQUIRED AT DIAPER DECK AND CHILD SEAT.
7. LOCAL ARCHITECT AND G.C. TO VERIFY ADA CONDITIONS WITH BUILDING OFFICIAL PRIOR TO CONSTRUCTION.

FINISH PLAN GENERAL NOTES

- A. All flooring materials to meet at center of doorway UNO.
- B. All flooring materials continue under casework to toe kick or under open counter to wall.
- C. Door frames to be painted <MFR>. Color: _____. Finish: Semi-gloss enamel, UNO.
- D. Refer to Reflected Ceiling Plan sheet(s) for soffit ceiling finishes.

FINISH PLAN - KEYNOTES


- 101 GENERAL CONTRACTOR SHALL INSTALL EXHAUST HOOD PACKAGE AS WELL AS PROVIDE ANY/ALL NECESSARY MATERIALS IN ORDER FOR PROPER HOOD OPERATION, SEE EQUIPMENT, MECHANICAL, AND ELECTRICAL.
- 102 PROVIDE 5/8" INTERIOR SANDED PLYWOOD IN LIEU OF GYPSUM WALL BOARD.
- 103 PROVIDE 5/8" CEMENT BOARD IN LIEU OF GYPSIUM WALL BOARD.
- 104 PROVIDE WD. BLOCKING AT WALL SHELVES COORDINATE EXTENT WITH EQUIPMENT PLAN. SEE DETAIL 13, SHEET A-501.
- 105 COUNTERS AND DECOR WALLS ARE PART OF COUNTER MILLWORK PKG. SEE EQUIPMENT SHEETS FOR PLAN, ELEVATIONS AND DETAILS.
- 106 CONCRETE STOOP, SEE STRUCTURAL.
- 107 GENERAL CONTRACTOR SHALL INSTALL WALK-IN COOLER/FREEZER PACKAGE. PROVIDE SEALED TRIM, FROM COOLER BOX TO SIDE WALL. VERIFY SEALING REQUIREMENTS PER LOCAL CODES. (COOLER TYPICALLY 1" FROM WALLS-REFER TO DETAILS 10, 11, 16, & 17 ON SHEET A-303.
- 108 MOP SINK, SEE DETAIL 14 ON SHEET INSERT A-501.
- 109 WATER FILTER SYSTEM, SEE EQUIPMENT PLAN AND SCHEDULES.
- 110 WATER METER LOCATION, SEE PLUMBING.
- 111 WATER HEATER, SEE PLUMBING.
- 112 ELECTRICAL PANEL, SEE ELECTRICAL - VERIFY W/ MANUFACTURER INSTALL REQUIREMENTS.
- 113 ELECTRICAL DISCONNECT AND METER SOCKET.
- 114 PHONE BOARD.
- 115 GAS METER
- 116 6" CONC. FILLED STEEL BOLLARD, SET INTO 12" CONC. PIER. MIN. 36"H & MIN. 36" DEEP.
- 117 PATIO TABLE LOCATIONS, INSTALL PER MANUFACTURERS RECOMMENDATIONS.
- 118 G.C. TO VERIFY AND PROVIDE BLOCKING PER MANUFACTURERS REQUIREMENTS.
- 119 G.C. TO PROVIDE AND INSTALL 2X8 HORIZONTAL WOOD BLOCKING (LET IN) TO STUDS BEHIND GYP. BD., CENTER OF BLOCKING 8'-11 1/2" AFF. MINIMUM LENGTH OF BLOCKING AS NOTED, END OF BLOCKING MUST LAND ON STUD.
- 120 OPTIONAL ROOF ACCESS LADDER.
- 121 PATIO RAILING, SEE DETAIL 5 INSERT SHEET AS-102.
- 122 COAT ROD & SHELF, PROVIDED & INSTALLED BY G.C.
- 123 EXTERIOR FIREPLACE ENCLOSURE (OPTIONAL), SEE DETAILS 1&2 SHEET A-304.
- 124 ROOF SCUPPER & DOWNSPOUT.
- 125 EXTERIOR RED SPOON, SEE EQUIPMENT PLAN, ELEVATIONS, WALL SECTIONS, AND & FOUNDATION PLAN.
- 126 SEE STRUCTURAL DRAWINGS FOR SHEARWALL REQUIREMENTS.
- 127 EQUIPMENT IN THIS AREA HAS CRITICAL INSTALLATION DIMENSIONS, SEE SHEET Q.105.
- 128 THIS AREA REQUIRES A DOUBLE LAYER OF GYP. BD. AND TRIMS, SEE INTERIOR ELEVATIONS AND DETAIL #5 ON SHEET A-501 FOR REQUIREMENTS.
- 129 HEAVY DUTY REFLECTIVE RUBBER SPEED BUMP

PAINT COLOR LEGEND

- PTD A COLOR: PRE FINISHED "U-HAUL BLACK"
- PTD D COLOR: PRE FINISHED "U-HAUL ORANGE"
- PTD P COLOR: SHERWIN-WILLIAMS "ULTRA WHITE"
- PTD Q COLOR: SHERWIN-WILLIAMS "ACCESSIBLE BEIGE"
- PRE-F PRE-FINISHED FROM MANUFACTURER


WALL FINISH LEGEND

- A GWB PAINTED WITH 4" RUBBER BASE (VCB). PAINT VARIES, VERIFY WITH OWNER DURING CONSTRUCTION.
- B GWB-WR WITH TILE-W BASE AND TILE-W/PTD P WALLS, REFER AB-401 FOR ELEVATIONS. PAINT COLOR AND FINISH TBD DURING CONSTRUCTION.
- A WALL FINISH.
- <48"H> <FULL HEIGHT> CORNER GUARD: MFR., MODEL: _____, COLOR: _____.
- <48"H> <FULL HEIGHT> END WALL CORNER GUARD: MFR., MODEL: _____, COLOR: _____.
- BG BUMPER GUARD: MFR., MODEL: _____, COLOR: _____.
- CR CRASH RAIL: MFR., MODEL: _____, COLOR: _____.

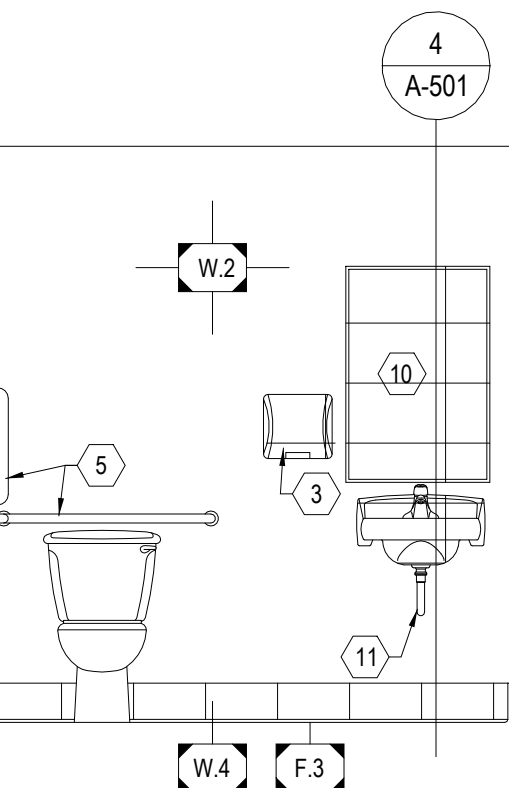


3 RESTROOM ELEVATION

0 4' 8' 12'
Scale is 3/8" = 1'-0" when printed full size.

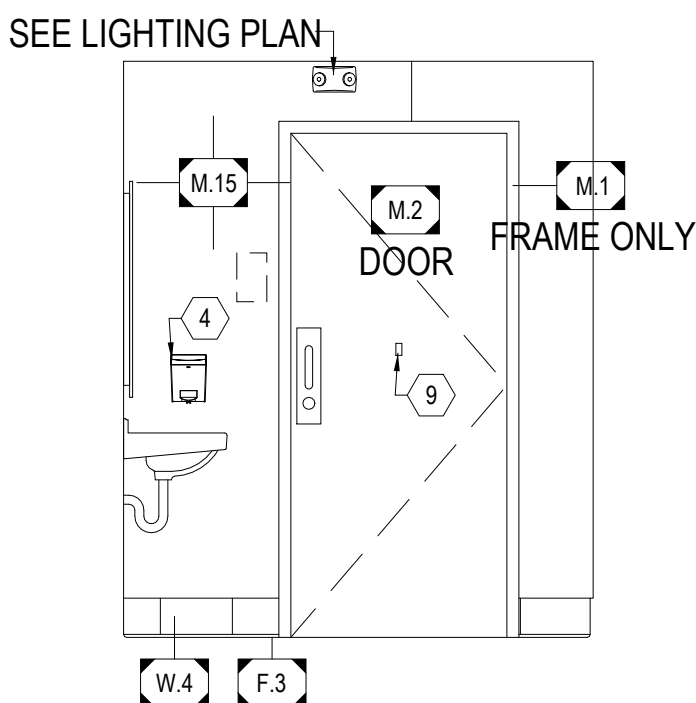


4 RESTROOM ELEVATION

0 4' 8' 12'
Scale is 3/8" = 1'-0" when printed full size.

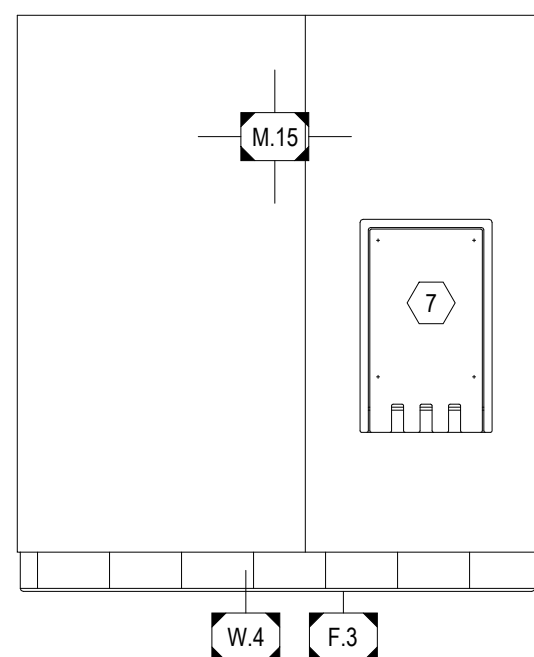


5 RESTROOM ELEVATION

0 4' 8' 12'
Scale is 3/8" = 1'-0" when printed full size.

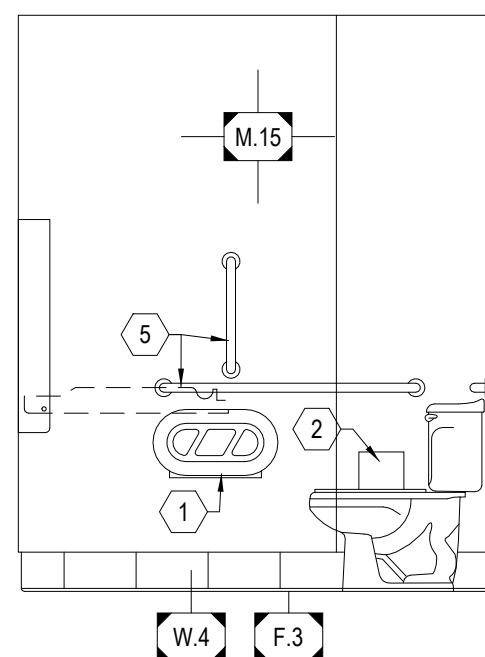


6 RESTROOM ELEVATION

0 4' 8' 12'
Scale is 3/8" = 1'-0" when printed full size.

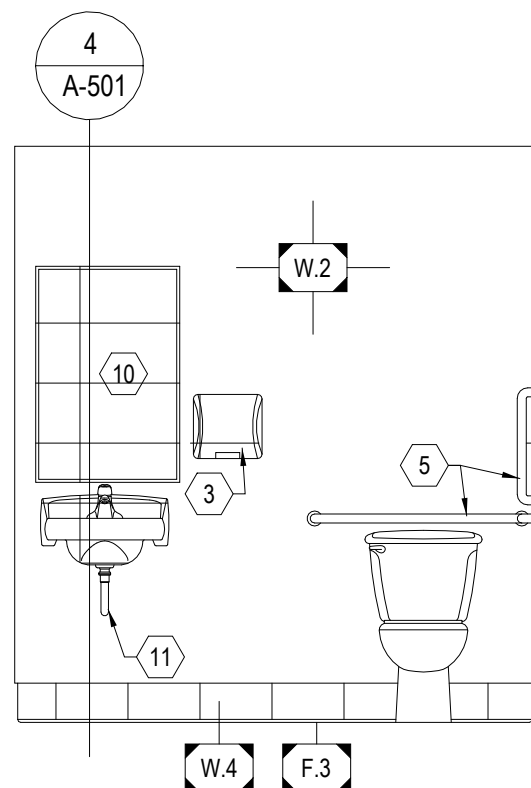


7 RESTROOM ELEVATION

0 4' 8' 12'
Scale is 3/8" = 1'-0" when printed full size.

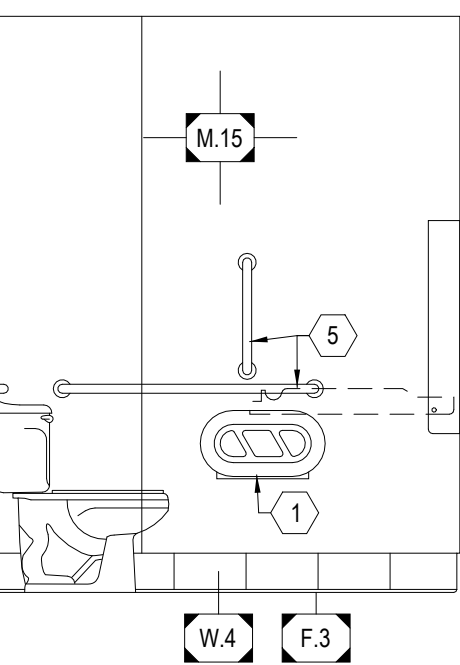


8 RESTROOM ELEVATION

0 4' 8' 12'
Scale is 3/8" = 1'-0" when printed full size.

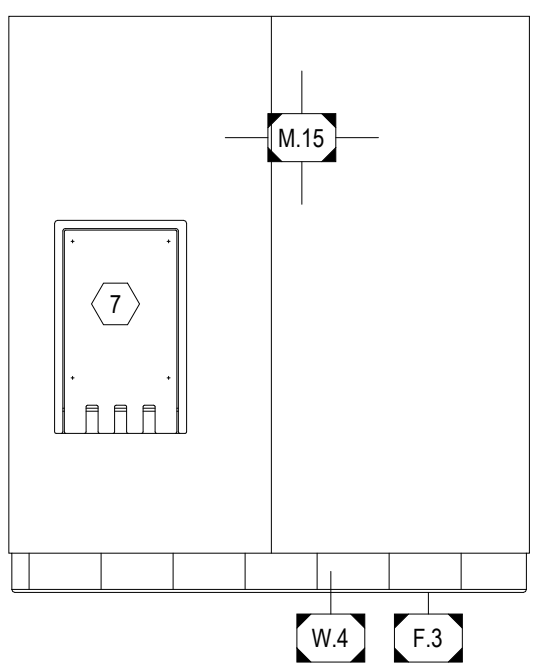

9 RESTROOM ELEVATION

0 4' 8' 12'
Scale is 3/8" = 1'-0" when printed full size.

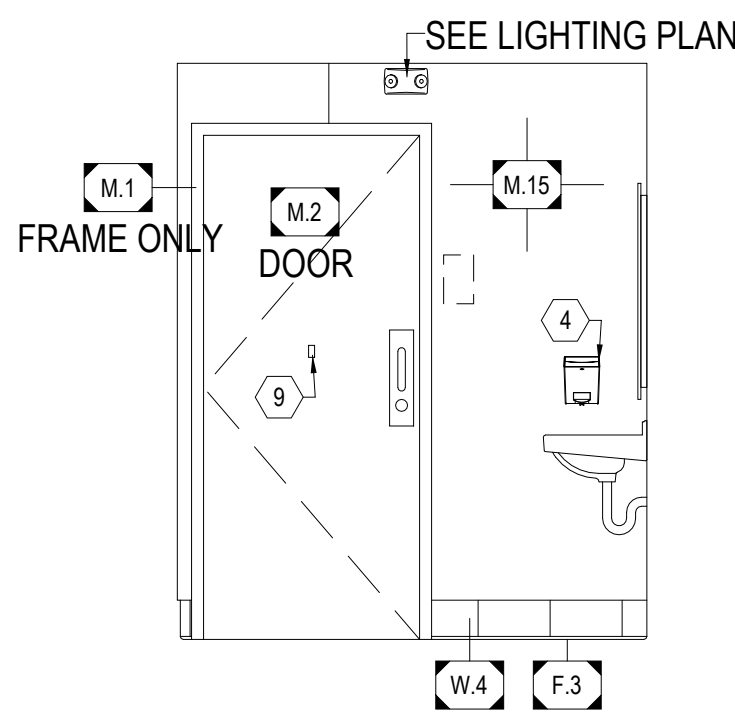

10 RESTROOM ELEVATION

0 4' 8' 12'
Scale is 3/8" = 1'-0" when printed full size.

REVISIONS:

DELTA DESCRIPTION DATE

DATE OF ISSUE: 04.13.2026

MA PROJECT NO: 0559-25

PROJECT PHASE: CD

DRAWN BY: RP

RESTROOM PLAN &
INTERIOR ELEVATIONS

A-703